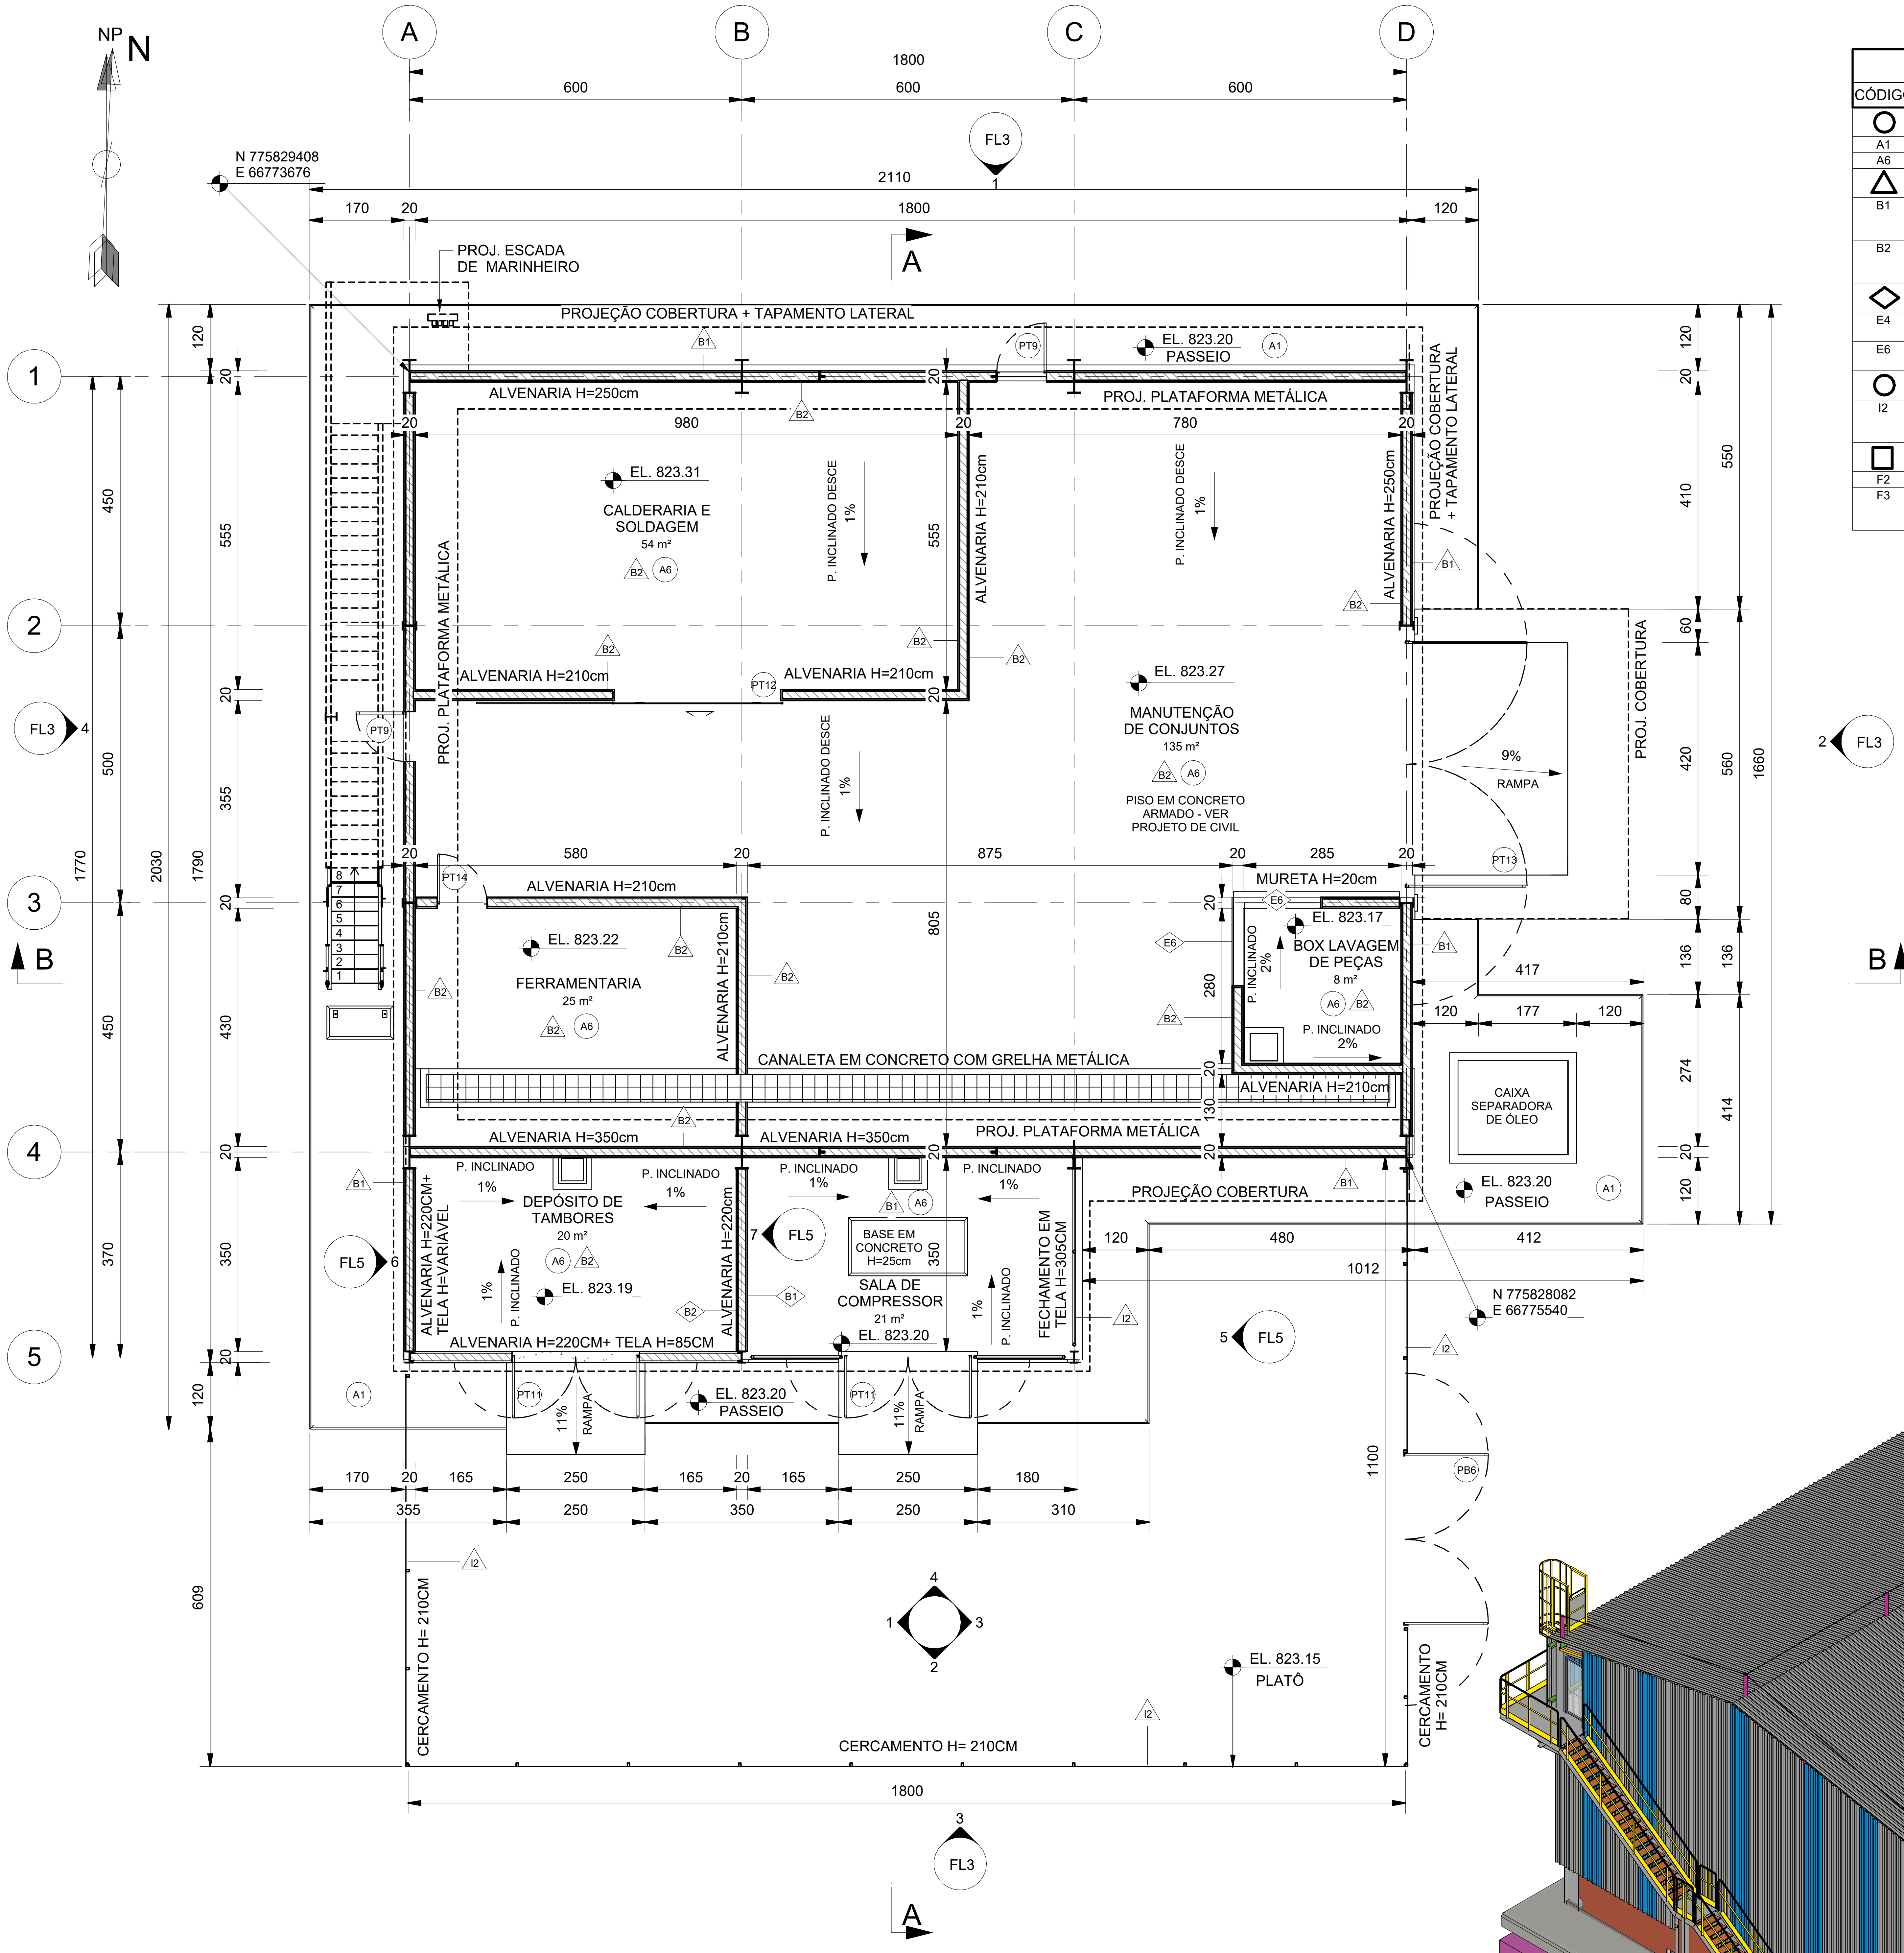

OFICINA AVANÇADA - PLANTA TÉCNICA

1 : 75

QUADRO ESPECIFICAÇÕES DE ACABAMENTOS

CÓDIGO	DESCRIÇÃO
○	PISOS
A1	PISO EM CONCRETO DESEMPENADO COM JUNTA SECA A CADA 1,20cm, ACABAMENTO VASSOURADO, ESP. 10cm
A6	PISO EM CONCRETO ARMADO, VER PROJETO DE CIVIL/CONCRETO
△	PAREDES
B1	ALVENARIA EM BLOCO DE CONCRETO REVESTIDA COM CHAPISCO, EMBOÇO E REBOCO E SELADOR ACRÍLICO, APLICAÇÃO DE DUAS DEMÃOS DE TINTA LÁTEX ACRÍLICA, ACABAMENTO ACETINADO, COR TERRACOTA, REF.: COR TERRACOTA (CÓD. R118) - SUVINIL OU SIMILAR
B2	ALVENARIA EM BLOCO DE CONCRETO REVESTIDA COM CHAPISCO, EMBOÇO E REBOCO E SELADOR ACRÍLICO, APLICAÇÃO DE DUAS DEMÃOS DE TINTA LÁTEX ACRÍLICA, ACABAMENTO ACETINADO, COR CINZA CLARO (RAL 7035) , REF.: SUVINIL OU SIMILAR
◇	SOLEIRAS, RODAPÉS E PEITORIS
E4	PEITORIL EM CONCRETO PRÉ-MOLDADO, ACABAMENTO LISO, COM PINGADEIRA, ESPESSURA 3cm, ASSENTADO COM ARGAMASSA COLANTE
E6	RODAPÉ EM CONCRETO PRÉ-MOLDADO, ACABAMENTO LISO, ESPESSURA 3cm, H=10cm, ASSENTADO COM ARGAMASSA COLANTE
○	CERCAMENTOS
I2	ALAMBRADO EM ESTRUTURA TUBULAR EM AÇO CARBONO DIÂM.=2", QUADRO FIXO COM TUBOS DIÂM.=1 '' E VEDAÇÃO EM TELA DE ARAME DE AÇO GALVANIZADO, MALHA QUADRADA 50mm (2 ''), FIO Nº 12 BWG E BARRA REDONDA ∅1/2''. APLICAÇÃO DE PINTURA ELETROSTÁTICA COR CINZA MÉDIO (RAL 7046), ACABAMENTO BRILHANTE
□	COBERTURAS
F2	TELHA TRAPEZOIDAL DE FIBRA DE VIDRO INCOLOR, VER PROJETO DE ESTRUTURAS METÁLICAS
F3	TELHA METÁLICA EM CHAPA DE AÇO GALVALUME TRAPEZOIDAL, H=40mm, ESPESSURA=65mm, ACABAMENTO EM PINTURA ESMALTE COR CINZA FACE EXTERNA, FACE INTERNA ACABAMENTO NATURAL, VER PROJETO DE ESTRUTURAS METÁLICAS

MAPA CHAVE

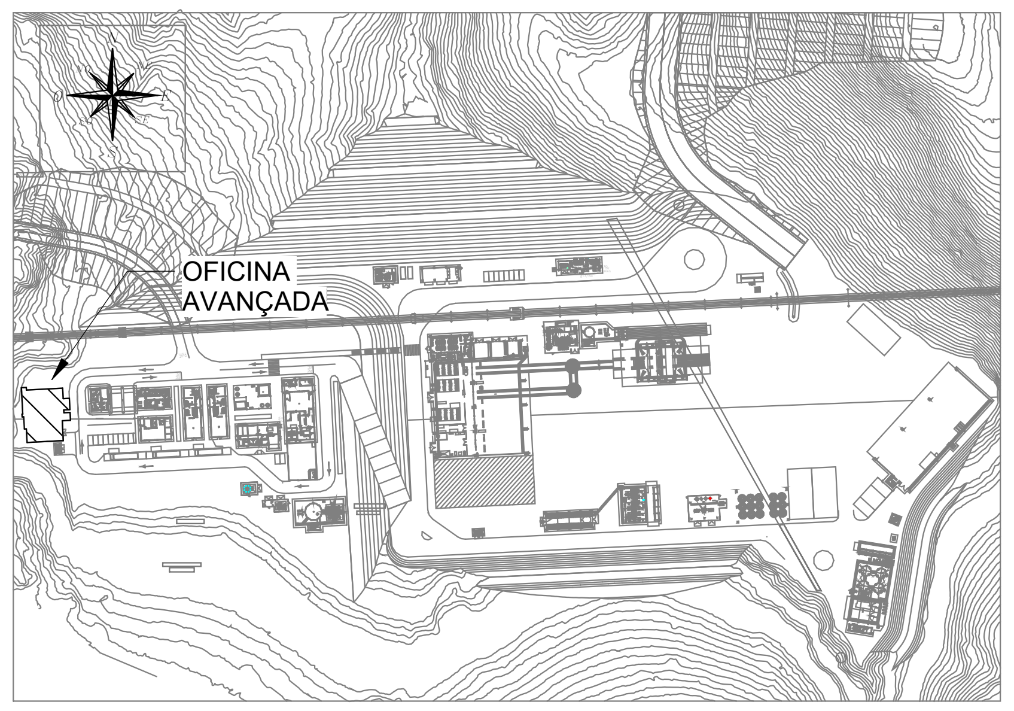

QUADRO DE ESQUADRIAS

CÓD.	LARGURA (cm)	ALTURA (cm)	DESCRIÇÃO	QTD.
PORTAS				
PB6	300	210	PORTÃO DE GIRO, 2 FOLHAS, ESTRUTURA TUBULAR EM AÇO CARBONO DIÂM.=1 1/2", QUADRO FIXO COM TUBOS DIÂM.=1 '' E VEDAÇÃO EM TELA DE ARAME DE AÇO GALVANIZADO, MALHA 2 '' , FIO Nº 12 BWG E BARRA REDONDA ∅1/2'' . TRINCO DESLIZANTE TIPO FERROLHO PARA CADEADO. APLICAÇÃO DE PINTURA COR CINZA MÉDIO (RAL 7046), ACABAMENTO BRILHANTE.	1
PT9	90	210	PORTÃO DE GIRO, 1 FOLHA, ESTRUTURA TUBULAR EM AÇO CARBONO DIÂM.=1 1/2", QUADRO FIXO COM TUBOS DIÂM.=1 '' E VEDAÇÃO EM TELA DE ARAME DE AÇO GALVANIZADO, MALHA 2 '' , FIO Nº 12 BWG E BARRA REDONDA ∅1/2'' . TRINCO DESLIZANTE TIPO FERROLHO PARA CADEADO. APLICAÇÃO DE PINTURA COR CINZA MÉDIO (RAL 7046), ACABAMENTO BRILHANTE.	3
PT11	220	300	PORTÃO DE GIRO, 2 FOLHAS, ESTRUTURA TUBULAR EM AÇO CARBONO DIÂM.=1 1/2", QUADRO FIXO COM TUBOS DIÂM.=1 '' E VEDAÇÃO EM TELA DE ARAME DE AÇO GALVANIZADO, MALHA 2 '' , FIO Nº 12 BWG E BARRA REDONDA ∅1/2'' . TRINCO DESLIZANTE TIPO FERROLHO PARA CADEADO. APLICAÇÃO DE PINTURA COR CINZA MÉDIO (RAL 7046), ACABAMENTO BRILHANTE.	2
PT12	300	210	PORTÃO DE CORRER, 1 FOLHA, ESTRUTURA TUBULAR EM AÇO CARBONO DIÂM.=1 1/2", QUADRO FIXO COM TUBOS DIÂM.=1 '' E VEDAÇÃO EM TELA DE ARAME DE AÇO GALVANIZADO, MALHA 2 '' , FIO Nº 12 BWG E BARRA REDONDA ∅1/2'' . TRINCO DESLIZANTE TIPO FERROLHO PARA CADEADO. APLICAÇÃO DE PINTURA COR CINZA MÉDIO (RAL 7046), ACABAMENTO BRILHANTE.	1
PT13	435	220	PORTÃO DE GIRO, 2 FOLHAS, ESTRUTURA TUBULAR EM AÇO CARBONO DIÂM.=1 1/2", QUADRO FIXO COM TUBOS DIÂM.=1 '' E VEDAÇÃO EM TELA DE ARAME DE AÇO GALVANIZADO, MALHA 2 '' , FIO Nº 12 BWG E BARRA REDONDA ∅1/2'' . TRINCO DESLIZANTE TIPO FERROLHO PARA CADEADO. APLICAÇÃO DE PINTURA COR CINZA MÉDIO (RAL 7046), ACABAMENTO BRILHANTE.	1
PT14	90	210	PORTÃO DE GIRO, 1 FOLHA, ESTRUTURA TUBULAR EM AÇO CARBONO DIÂM.=1 1/2", QUADRO FIXO COM TUBOS DIÂM.=1 '' E VEDAÇÃO EM TELA DE ARAME DE AÇO GALVANIZADO, MALHA 2 '' , FIO Nº 12 BWG E BARRA REDONDA ∅1/2'' . TRINCO DESLIZANTE TIPO FERROLHO PARA CADEADO. APLICAÇÃO DE PINTURA COR CINZA MÉDIO (RAL 7046), ACABAMENTO BRILHANTE.	1

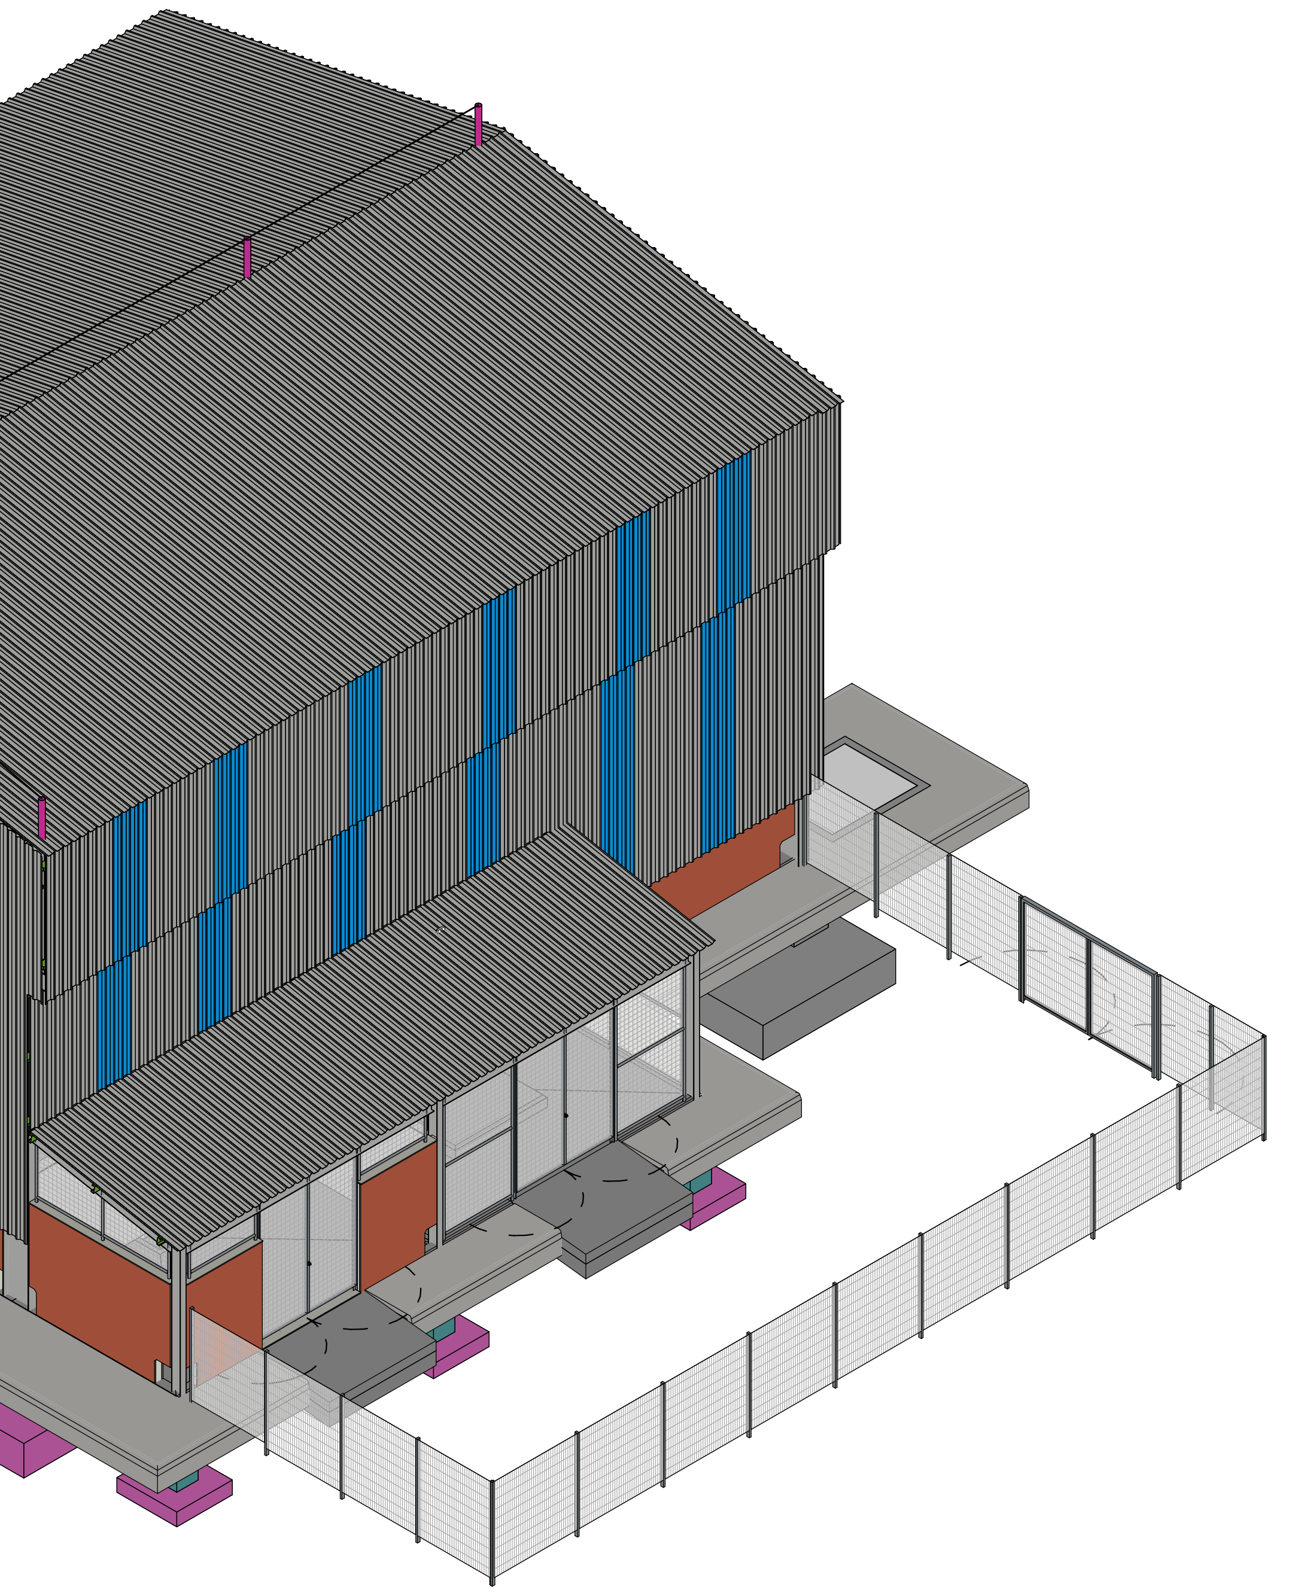

PERSPECTIVA

CODIFICAÇÃO AWP – ADVANCED WORK PACKAGING

CWA	CÓDIGOS:	CWA 001 - PLATÔ DOS PRÉDIOS OPERACIONAIS
CWP	CÓDIGOS:	CWP 007 - OFICINA AVANÇADA G1342ED08-CWA 001-G-MT-0001.007-CWP 007
EWP	CÓDIGOS:	G1342ED08-CWA 001-G-MT-0001.007-EWP 007

NOTAS

1- DIMENSÕES EM CENTÍMETROS, ELEVAÇÕES E COORDENADAS EM METRO, SALVO INDICAÇÃO EM CONTRÁRIO;
2 - AS ELEVAÇÕES APRESENTADAS EM PROJETO CORRESPONDEM AO NÍVEL DO PISO ACABADO;
3 - PARA ESPECIFICAÇÕES DETALHADAS DOS MATERIAIS E ACABAMENTOS, VER CADERNO DE ESPECIFICAÇÕES DA SAMARCO (DOCUMENTO Nº T000000-G-6NT004);
4 - PARA AS PAREDES EXTERNAS E INTERNAS DA OFICINA SERÃO UTILIZADOS BLOCOS DE CONCRETO COM ESPESSURA DE 14cm.
5 - A ELEVAÇÃO 0,00 NO PROJETO CORRESPONDE À COTA +823,00 DO PROJETO DE INFRAESTRUTURA (DOCUMENTO SAMARCO Nº G134448-O-1000105).
6 - O ESCOPO DA DISCIPLINA DE ARQUITETURA NA OFICINA AVANÇADA SE LIMITA AS DEFINIÇÕES DOS CERCAMENTOS, ALAMBRADOS, ESQUADRIAS, ALVENARIAS E ACABAMENTOS. A DISPOSIÇÃO DOS AMBIENTES INTERNOS, O LAYOUT, E OS ACESSOS FORAM DEFINIDOS PELA MECÂNICA.
7 - AS ALVENARIAS DE DIVISÃO ENTRE O DEPÓSITO DE TAMBORES E O COMPRESSOR, E ENTRE O DEPÓSITO E A OFICINA DEVERÃO POSSUIR PROPRIEDADES CORTA-FOGO, CONFORME IT-06 DO CBMMG. DESTA FORMA, DEVERÃO SER EXECUTADAS COM BLOCO DE CONCRETO DE 14cm DE ESPESSURA, COM UMA CAMADA DE CHAPISCO E EMBOÇO DE NO MÍNIMO 1,5cm.
8 - PARA LAYOUT DA OFICINA AVANÇADA, VER DOCUMENTO MECÂNICA NºG134211-M-100039.
9 - A ESCADA DE MARINHEIRO PARA ACESSO À COBERTURA DEVERÁ SEGUIR AS PREMISSAS DOCUMENTO DE SEGURANÇA DA SAMARCO Nº T000002-S-2PS004;

DESENHOS DE REFERÊNCIA

1 - IMPLANTAÇÃO DA ARQUITETURA - DOC. Nº G134140-C-800038
2 - DESENHOS COMPLEMENTARES G134240-C-800031 / G134240-C-800032 / G134240-C-8000XX / G134240-C-8000XX
3 - DETALHAMENTO DE ESQUADRIAS - DOC. Nº G130000-C-800001 / G130000-C-800002 / G130000-C-800003 / G130000-C-800004

ESPESSURA DE LINHAS DA SAMARCO
1 – RED – 0,10mm
2 – YELLOW – 0,5mm
3 – GREEN – 0,20mm
4 – CYAN – 0,30mm
5 – BLUE – 0,15mm
6 – MAGENTA – 0,60mm
7 – WHITE – 0,40mm
8 – CINZA – 0,80mm

ESPESSURA DE LINHAS EXTRAS ADOTADAS NESTE DESENHO SAMARCO
17 18 19
20 21 22
23 24 25

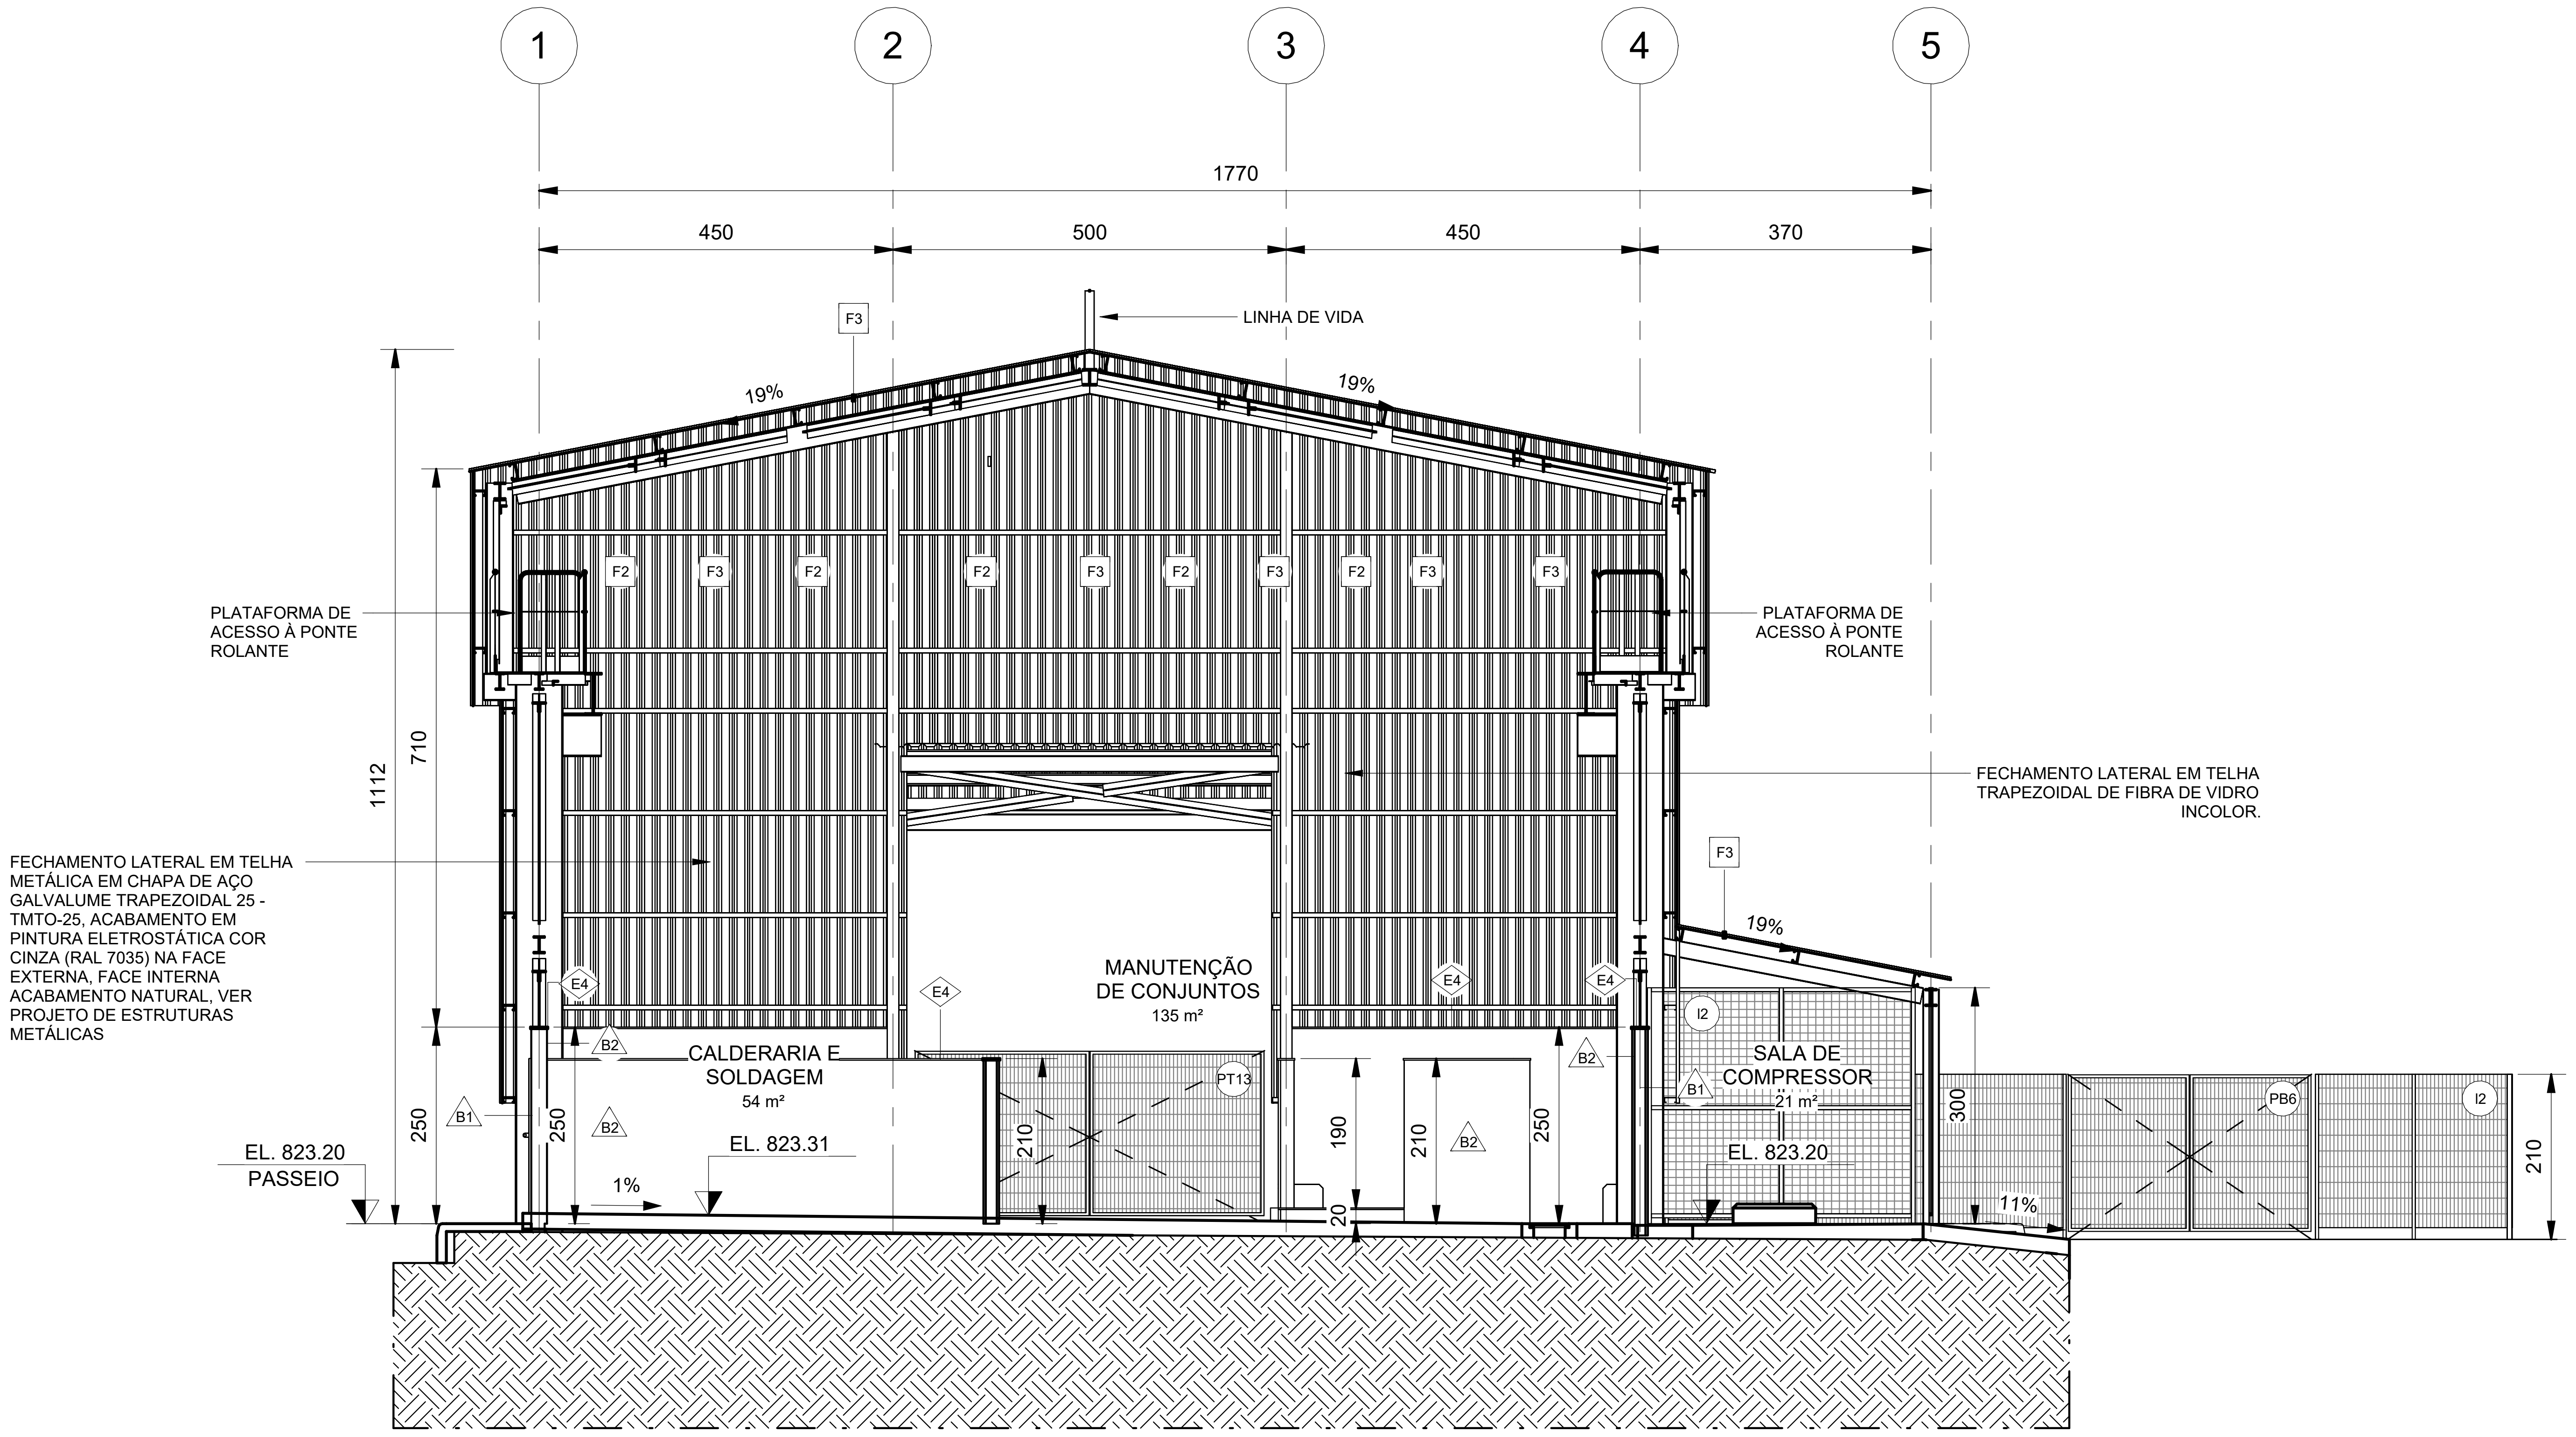
1
2
3
4
5
1770
450
500
450
370
F3
LINHA DE VIDA
19%
19%
F2
F3
F2
F2
F3
F2
F3
F2
F3
F3
PLATAFORMA DE ACESSO À PONTE ROLANTE
PLATAFORMA DE ACESSO À PONTE ROLANTE
1112
710
FECHAMENTO LATERAL EM TELHA TRAPEZOIDAL DE FIBRA DE VIDRO INCOLOR.
FECHAMENTO LATERAL EM TELHA METÁLICA EM CHAPA DE AÇO GALVALUME TRAPEZOIDAL 25 - TMTO-25, ACABAMENTO EM PINTURA ELETROSTÁTICA COR CINZA (RAL 7035) NA FACE EXTERNA, FACE INTERNA ACABAMENTO NATURAL, VER PROJETO DE ESTRUTURAS METÁLICAS
F3
19%
E4
E4
E4
E4
MANUTENÇÃO DE CONJUNTOS
135 m²
CALDERARIA E SOLDAGEM
54 m²
B2
B2
PT13
I2
SALA DE COMPRESSOR
21 m²
B1
B1
B2
B2
PB6
I2
EL. 823.20
PASSEIO
250
250
1%
EL. 823.31
210
190
20
210
250
300
EL. 823.20
11%
210

CORTE AA
1 : 75

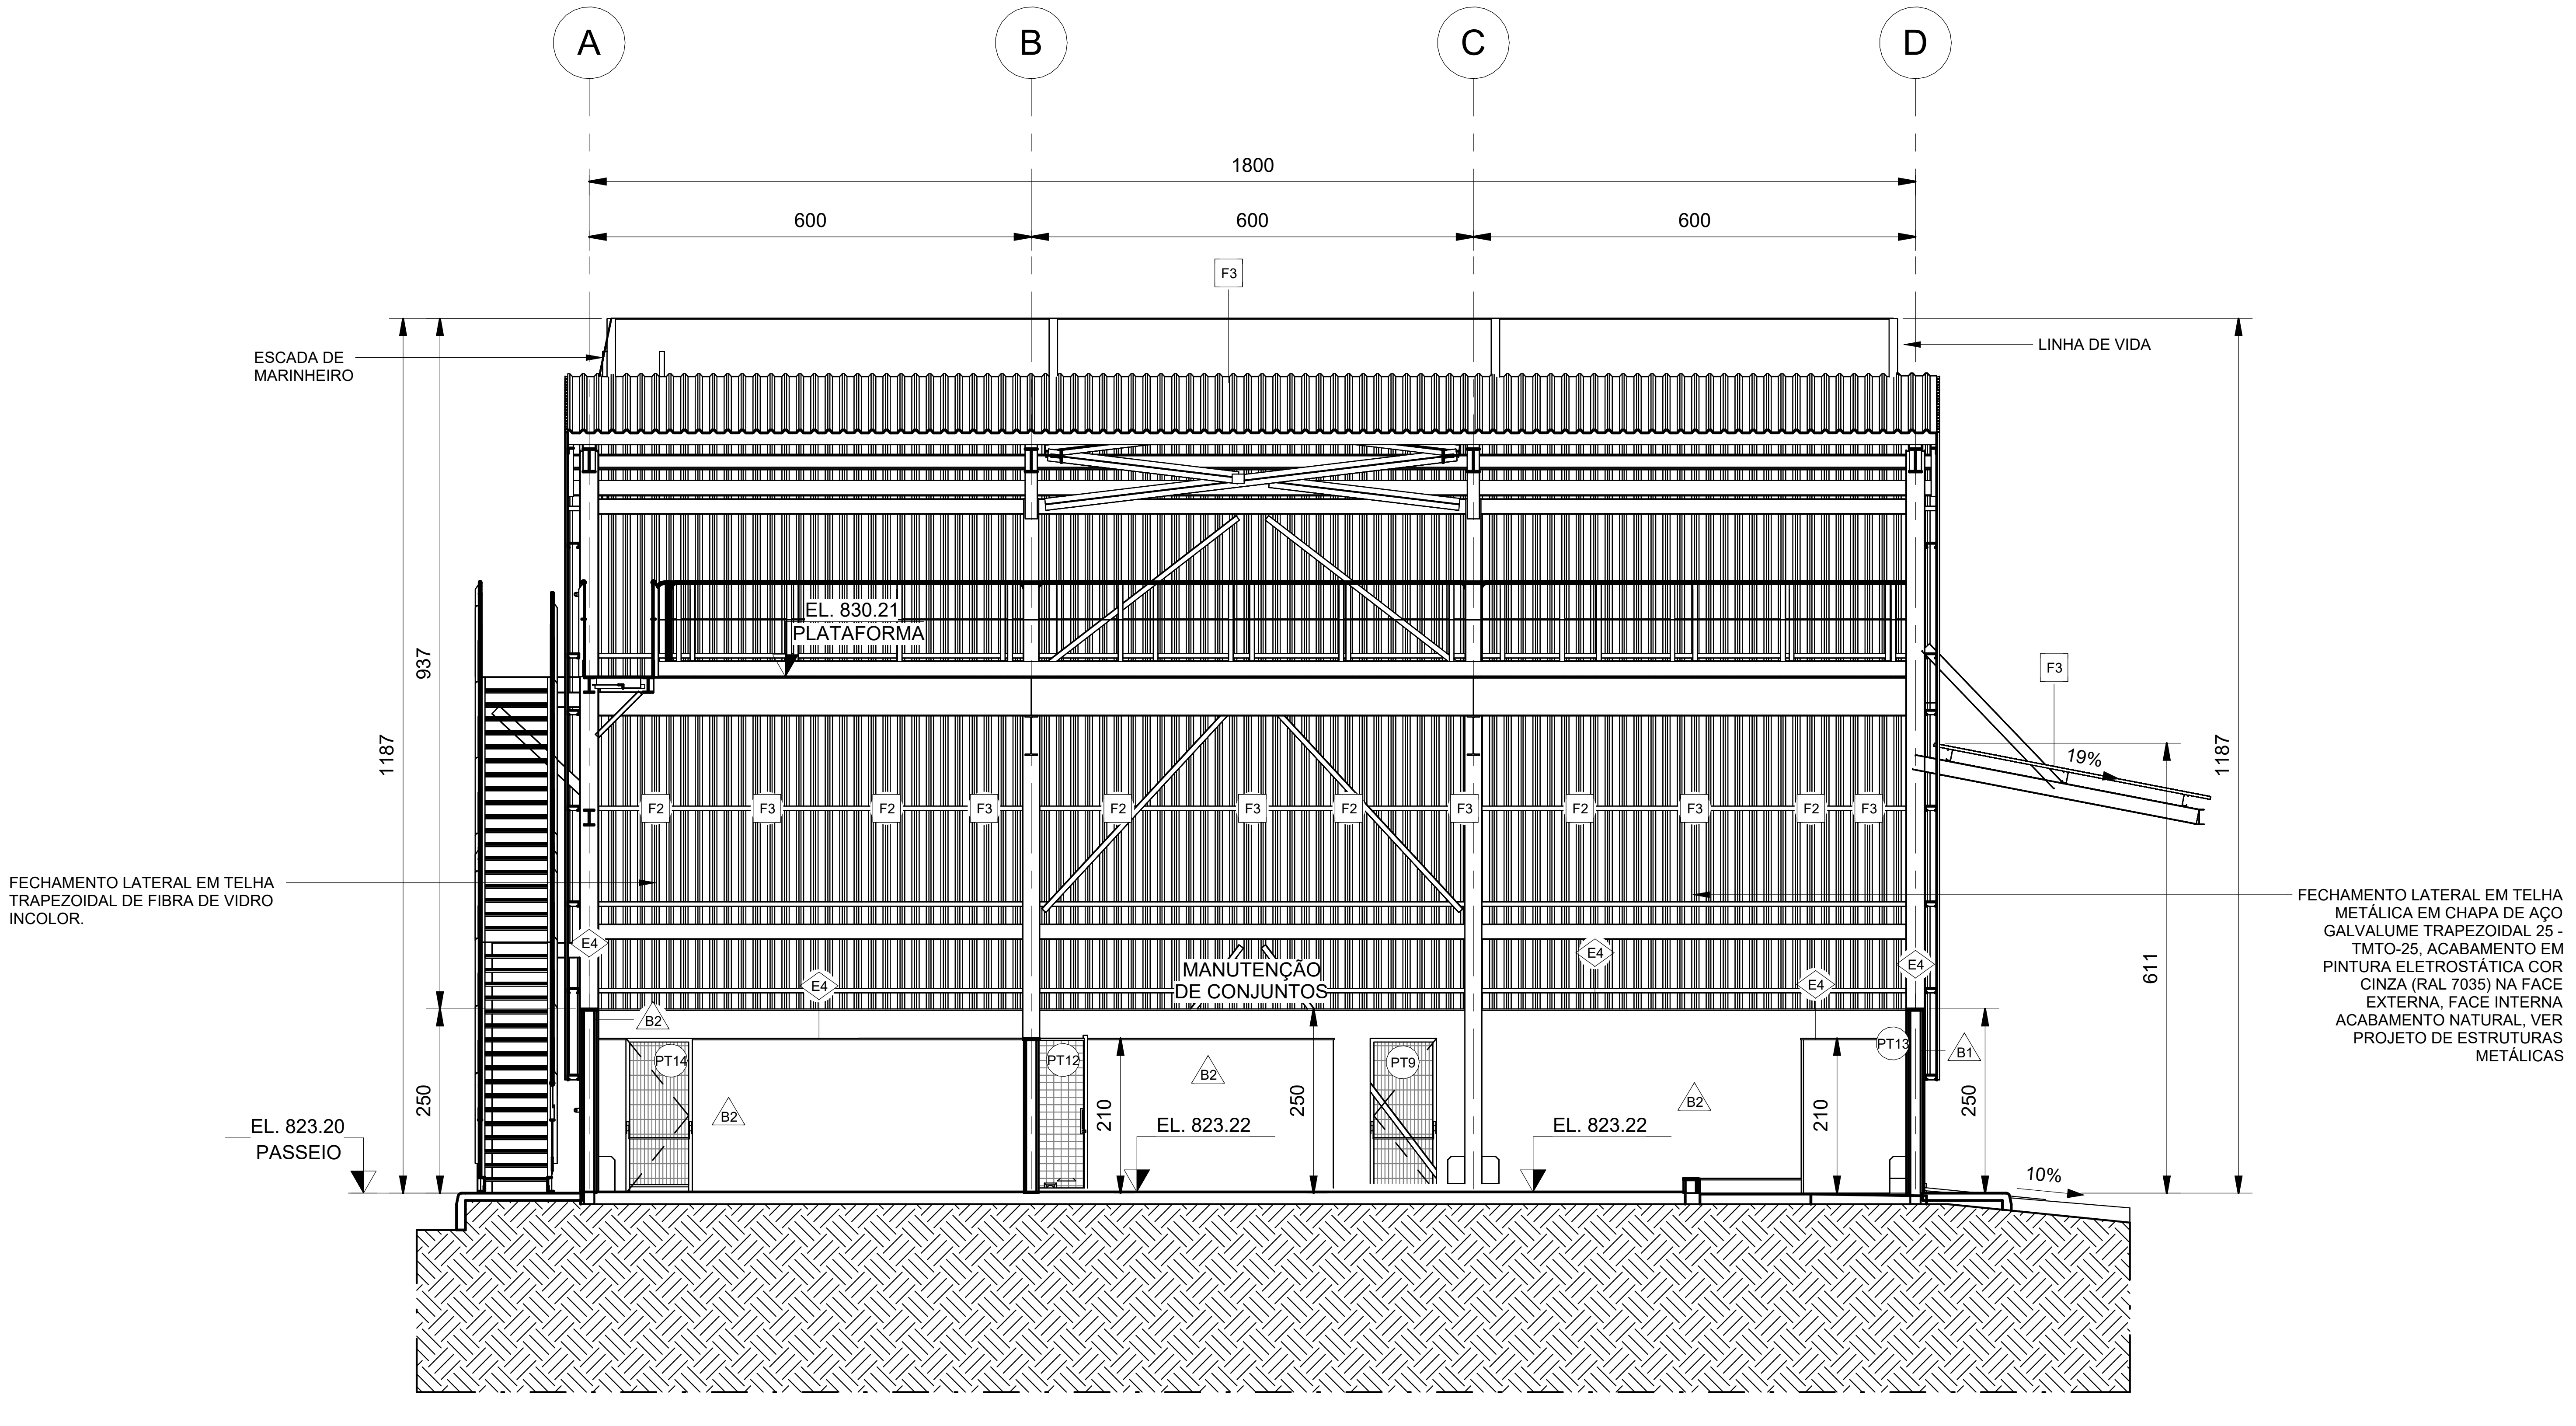
A
B
C
D
1800
600
600
600
F3
ESCADA DE MARINHEIRO
LINHA DE VIDA
EL. 830.21
PLATAFORMA
937
1187
F3
19%
1187
F2
F3
F2
F3
F2
F3
F2
F3
F2
F3
F2
F3
FECHAMENTO LATERAL EM TELHA TRAPEZOIDAL DE FIBRA DE VIDRO INCOLOR.
FECHAMENTO LATERAL EM TELHA METÁLICA EM CHAPA DE AÇO GALVALUME TRAPEZOIDAL 25 - TMTO-25, ACABAMENTO EM PINTURA ELETROSTÁTICA COR CINZA (RAL 7035) NA FACE EXTERNA, FACE INTERNA ACABAMENTO NATURAL, VER PROJETO DE ESTRUTURAS METÁLICAS
E4
E4
E4
E4
E4
MANUTENÇÃO DE CONJUNTOS
611
B2
PT14
PT12
B2
PT9
PT13
B1
B2
B2
EL. 823.20
PASSEIO
250
210
EL. 823.22
250
EL. 823.22
210
250
10%

CORTE BB
1 : 75

QUADRO DE ESQUADRIAS

CÓD.	LARGURA (cm)	ALTURA (cm)	DESCRIÇÃO	QTD.
			PORTAS	
PB6	300	210	PORTÃO DE GIRO, 2 FOLHAS, ESTRUTURA TUBULAR EM AÇO CARBONO DIÂM.=1 1/2", QUADRO FIXO COM TUBOS DIÂM.=1 '' E VEDAÇÃO EM TELA DE ARAME DE AÇO GALVANIZADO, MALHA 2 '' , FIO Nº 12 BWG E BARRA REDONDA ∅1/2'' . TRINCO DESLIZANTE TIPO FERROLHO PARA CADEADO. APLICAÇÃO DE PINTURA COR CINZA MÉDIO (RAL 7046), ACABAMENTO BRILHANTE.	1
PT9	90	210	PORTÃO DE GIRO, 1 FOLHA, ESTRUTURA TUBULAR EM AÇO CARBONO DIÂM.=1 1/2", QUADRO FIXO COM TUBOS DIÂM.=1 '' E VEDAÇÃO EM TELA DE ARAME DE AÇO GALVANIZADO, MALHA 2 '' , FIO Nº 12 BWG E BARRA REDONDA ∅1/2'' . TRINCO DESLIZANTE TIPO FERROLHO PARA CADEADO. APLICAÇÃO DE PINTURA COR CINZA MÉDIO (RAL 7046), ACABAMENTO BRILHANTE.	3
PT11	220	300	PORTÃO DE GIRO, 2 FOLHAS, ESTRUTURA TUBULAR EM AÇO CARBONO DIÂM.=1 1/2", QUADRO FIXO COM TUBOS DIÂM.=1 '' E VEDAÇÃO EM TELA DE ARAME DE AÇO GALVANIZADO, MALHA 2 '' , FIO Nº 12 BWG E BARRA REDONDA ∅1/2'' . TRINCO DESLIZANTE TIPO FERROLHO PARA CADEADO. APLICAÇÃO DE PINTURA COR CINZA MÉDIO (RAL 7046), ACABAMENTO BRILHANTE.	1
PT12	300	210	PORTÃO DE CORRER, 1 FOLHA, ESTRUTURA TUBULAR EM AÇO CARBONO DIÂM.=1 1/2", QUADRO FIXO COM TUBOS DIÂM.=1 '' E VEDAÇÃO EM TELA DE ARAME DE AÇO GALVANIZADO, MALHA 2 '' , FIO Nº 12 BWG E BARRA REDONDA ∅1/2'' . TRINCO DESLIZANTE TIPO FERROLHO PARA CADEADO. APLICAÇÃO DE PINTURA COR CINZA MÉDIO (RAL 7046), ACABAMENTO BRILHANTE.	1
PT13	435	220	PORTÃO DE GIRO, 2 FOLHAS, ESTRUTURA TUBULAR EM AÇO CARBONO DIÂM.=1 1/2", QUADRO FIXO COM TUBOS DIÂM.=1 '' E VEDAÇÃO EM TELA DE ARAME DE AÇO GALVANIZADO, MALHA 2 '' , FIO Nº 12 BWG E BARRA REDONDA ∅1/2'' . TRINCO DESLIZANTE TIPO FERROLHO PARA CADEADO. APLICAÇÃO DE PINTURA COR CINZA MÉDIO (RAL 7046), ACABAMENTO BRILHANTE.	1
PT14	90	210	PORTÃO DE GIRO, 1 FOLHA, ESTRUTURA TUBULAR EM AÇO CARBONO DIÂM.=1 1/2", QUADRO FIXO COM TUBOS DIÂM.=1 '' E VEDAÇÃO EM TELA DE ARAME DE AÇO GALVANIZADO, MALHA 2 '' , FIO Nº 12 BWG E BARRA REDONDA ∅1/2'' . TRINCO DESLIZANTE TIPO FERROLHO PARA CADEADO. APLICAÇÃO DE PINTURA COR CINZA MÉDIO (RAL 7046), ACABAMENTO BRILHANTE.	1

QUADRO ESPECIFICAÇÕES DE ACABAMENTOS

CÓDIGO	DESCRIÇÃO
○	PISOS
A1	PISO EM CONCRETO DESEMPENADO COM JUNTA SECA A CADA 1,20cm, ACABAMENTO VASSOURADO, ESP. 10cm
A6	PISO EM CONCRETO ARMADO, VER PROJETO DE CIVIL/CONCRETO
△	PAREDES
B1	ALVENARIA EM BLOCO DE CONCRETO REVESTIDA COM CHAPISCO, EMBOÇO E REBOCO E SELADOR ACRÍLICO, APLICAÇÃO DE DUAS DEMÃOS DE TINTA LÁTEX ACRÍLICA, ACABAMENTO ACETINADO, COR TERRACOTA, REF.: COR TERRACOTA (CÓD. R118) - SUVINIL OU SIMILAR
B2	ALVENARIA EM BLOCO DE CONCRETO REVESTIDA COM CHAPISCO, EMBOÇO E REBOCO E SELADOR ACRÍLICO, APLICAÇÃO DE DUAS DEMÃOS DE TINTA LÁTEX ACRÍLICA, ACABAMENTO ACETINADO, COR CINZA CLARO (RAL 7035) , REF.: SUVINIL OU SIMILAR
◇	SOLEIRAS, RODAPÉS E PEITORIS
E4	PEITORIL EM CONCRETO PRÉ-MOLDADO, ACABAMENTO LISO, COM PINGADEIRA, ESPESSURA 3cm, ASSENTADO COM ARGAMASSA COLANTE
E6	RODAPÉ EM CONCRETO PRÉ-MOLDADO, ACABAMENTO LISO, ESPESSURA 3cm, H=10cm, ASSENTADO COM ARGAMASSA COLANTE
○	CERCAMENTOS
I2	ALAMBRADO EM ESTRUTURA TUBULAR EM AÇO CARBONO DIÂM.=2", QUADRO FIXO COM TUBOS DIÂM.=1 '' E VEDAÇÃO EM TELA DE ARAME DE AÇO GALVANIZADO, MALHA QUADRADA 50mm (2 ''), FIO Nº 12 BWG E BARRA REDONDA ∅1/2''. APLICAÇÃO DE PINTURA ELETROSTÁTICA COR CINZA MÉDIO (RAL 7046), ACABAMENTO BRILHANTE
□	COBERTURAS
F2	TELHA TRAPEZOIDAL DE FIBRA DE VIDRO INCOLOR, VER PROJETO DE ESTRUTURAS METÁLICAS
F3	TELHA METÁLICA EM CHAPA DE AÇO GALVALUME TRAPEZOIDAL, H=40mm, ESPESSURA=65mm, ACABAMENTO EM PINTURA ESMALTE COR CINZA FACE EXTERNA, FACE INTERNA ACABAMENTO NATURAL, VER PROJETO DE ESTRUTURAS METÁLICAS

CODIFICAÇÃO AWP – ADVANCED WORK PACKAGING

CWA	CÓDIGOS:	CWA 001 - PLATÔ DOS PRÉDIOS OPERACIONAIS
CWP	CÓDIGOS:	CWP 007 - OFICINA AVANÇADA G1342ED08-CWA 001-G-MT-0001.007-CWP 007
EWP	CÓDIGOS:	G1342ED08-CWA 001-G-MT-0001.007-EWP 007

NOTAS

1- DIMENSÕES EM CENTÍMETROS, ELEVAÇÕES E COORDENADAS EM METRO, SALVO INDICAÇÃO EM CONTRÁRIO;
2 - AS ELEVAÇÕES APRESENTADAS EM PROJETO CORRESPONDEM AO NÍVEL DO PISO ACABADO;
3 - PARA ESPECIFICAÇÕES DETALHADAS DOS MATERIAIS E ACABAMENTOS, VER CADERNO DE ESPECIFICAÇÕES DA SAMARCO (DOCUMENTO Nº T000000-G-6NT004);
4 - PARA AS PAREDES EXTERNAS E INTERNAS DA OFICINA SERÃO UTILIZADOS BLOCOS DE CONCRETO COM ESPESSURA DE 14cm.
5 - A ELEVAÇÃO 0,00 NO PROJETO CORRESPONDE À COTA +823,00 DO PROJETO DE INFRAESTRUTURA (DOCUMENTO SAMARCO Nº G134448-O-1000105).
6 - O ESCOPO DA DISCIPLINA DE ARQUITETURA NA OFICINA AVANÇADA SE LIMITA AS DEFINIÇÕES DOS CERCAMENTOS, ALAMBRADOS, ESQUADRIAS, ALVENARIAS E ACABAMENTOS. A DISPOSIÇÃO DOS AMBIENTES INTERNOS, O LAYOUT, E OS ACESSOS FORAM DEFINIDOS PELA MECÂNICA.
7 - AS ALVENARIAS DE DIVISÃO ENTRE O DEPÓSITO DE TAMBORES E O COMPRESSOR, E ENTRE O DEPÓSITO E A OFICINA DEVERÃO POSSUIR PROPRIEDADES CORTA-FOGO, CONFORME IT-06 DO CBMMG. DESTA FORMA, DEVERÃO SER EXECUTADAS COM BLOCO DE CONCRETO DE 14cm DE ESPESSURA, COM UMA CAMADA DE CHAPISCO E EMBOÇO DE NO MÍNIMO 1,5cm.
8 - PARA LAYOUT DA OFICINA AVANÇADA, VER DOCUMENTO MECÂNICA NºG134211-M-100039.
9 - A ESCADA DE MARINHEIRO PARA ACESSO À COBERTURA DEVERÁ SEGUIR AS PREMISSAS DOCUMENTO DE SEGURANÇA DA SAMARCO Nº T000002-S-2PS004;

DESENHOS DE REFERÊNCIA

1 - IMPLANTAÇÃO DA ARQUITETURA - DOC. Nº G134140-C-800038
2 - DESENHOS COMPLEMENTARES G134240-C-800030 / G134240-C-800032 / G134240-C-8000XX / G134240-C-8000XX
3 - DETALHAMENTO DE ESQUADRIAS - DOC. Nº G130000-C-800001 / G130000-C-800002 / G130000-C-800003 / G130000-C-800004

ESPESSURA DE LINHAS DA SAMARCO
1 – RED – 0,10mm
2 – YELLOW – 0,5mm
3 – GREEN – 0,20mm
4 – CYAN – 0,30mm
5 – BLUE – 0,15mm
6 – MAGENTA – 0,60mm
7 – WHITE – 0,40mm
8 – CINZA – 0,80mm

ESPESSURA DE LINHAS EXTRAS ADOTADAS NESTE DESENHO SAMARCO
17 18 19
20 21 22
23 24 25

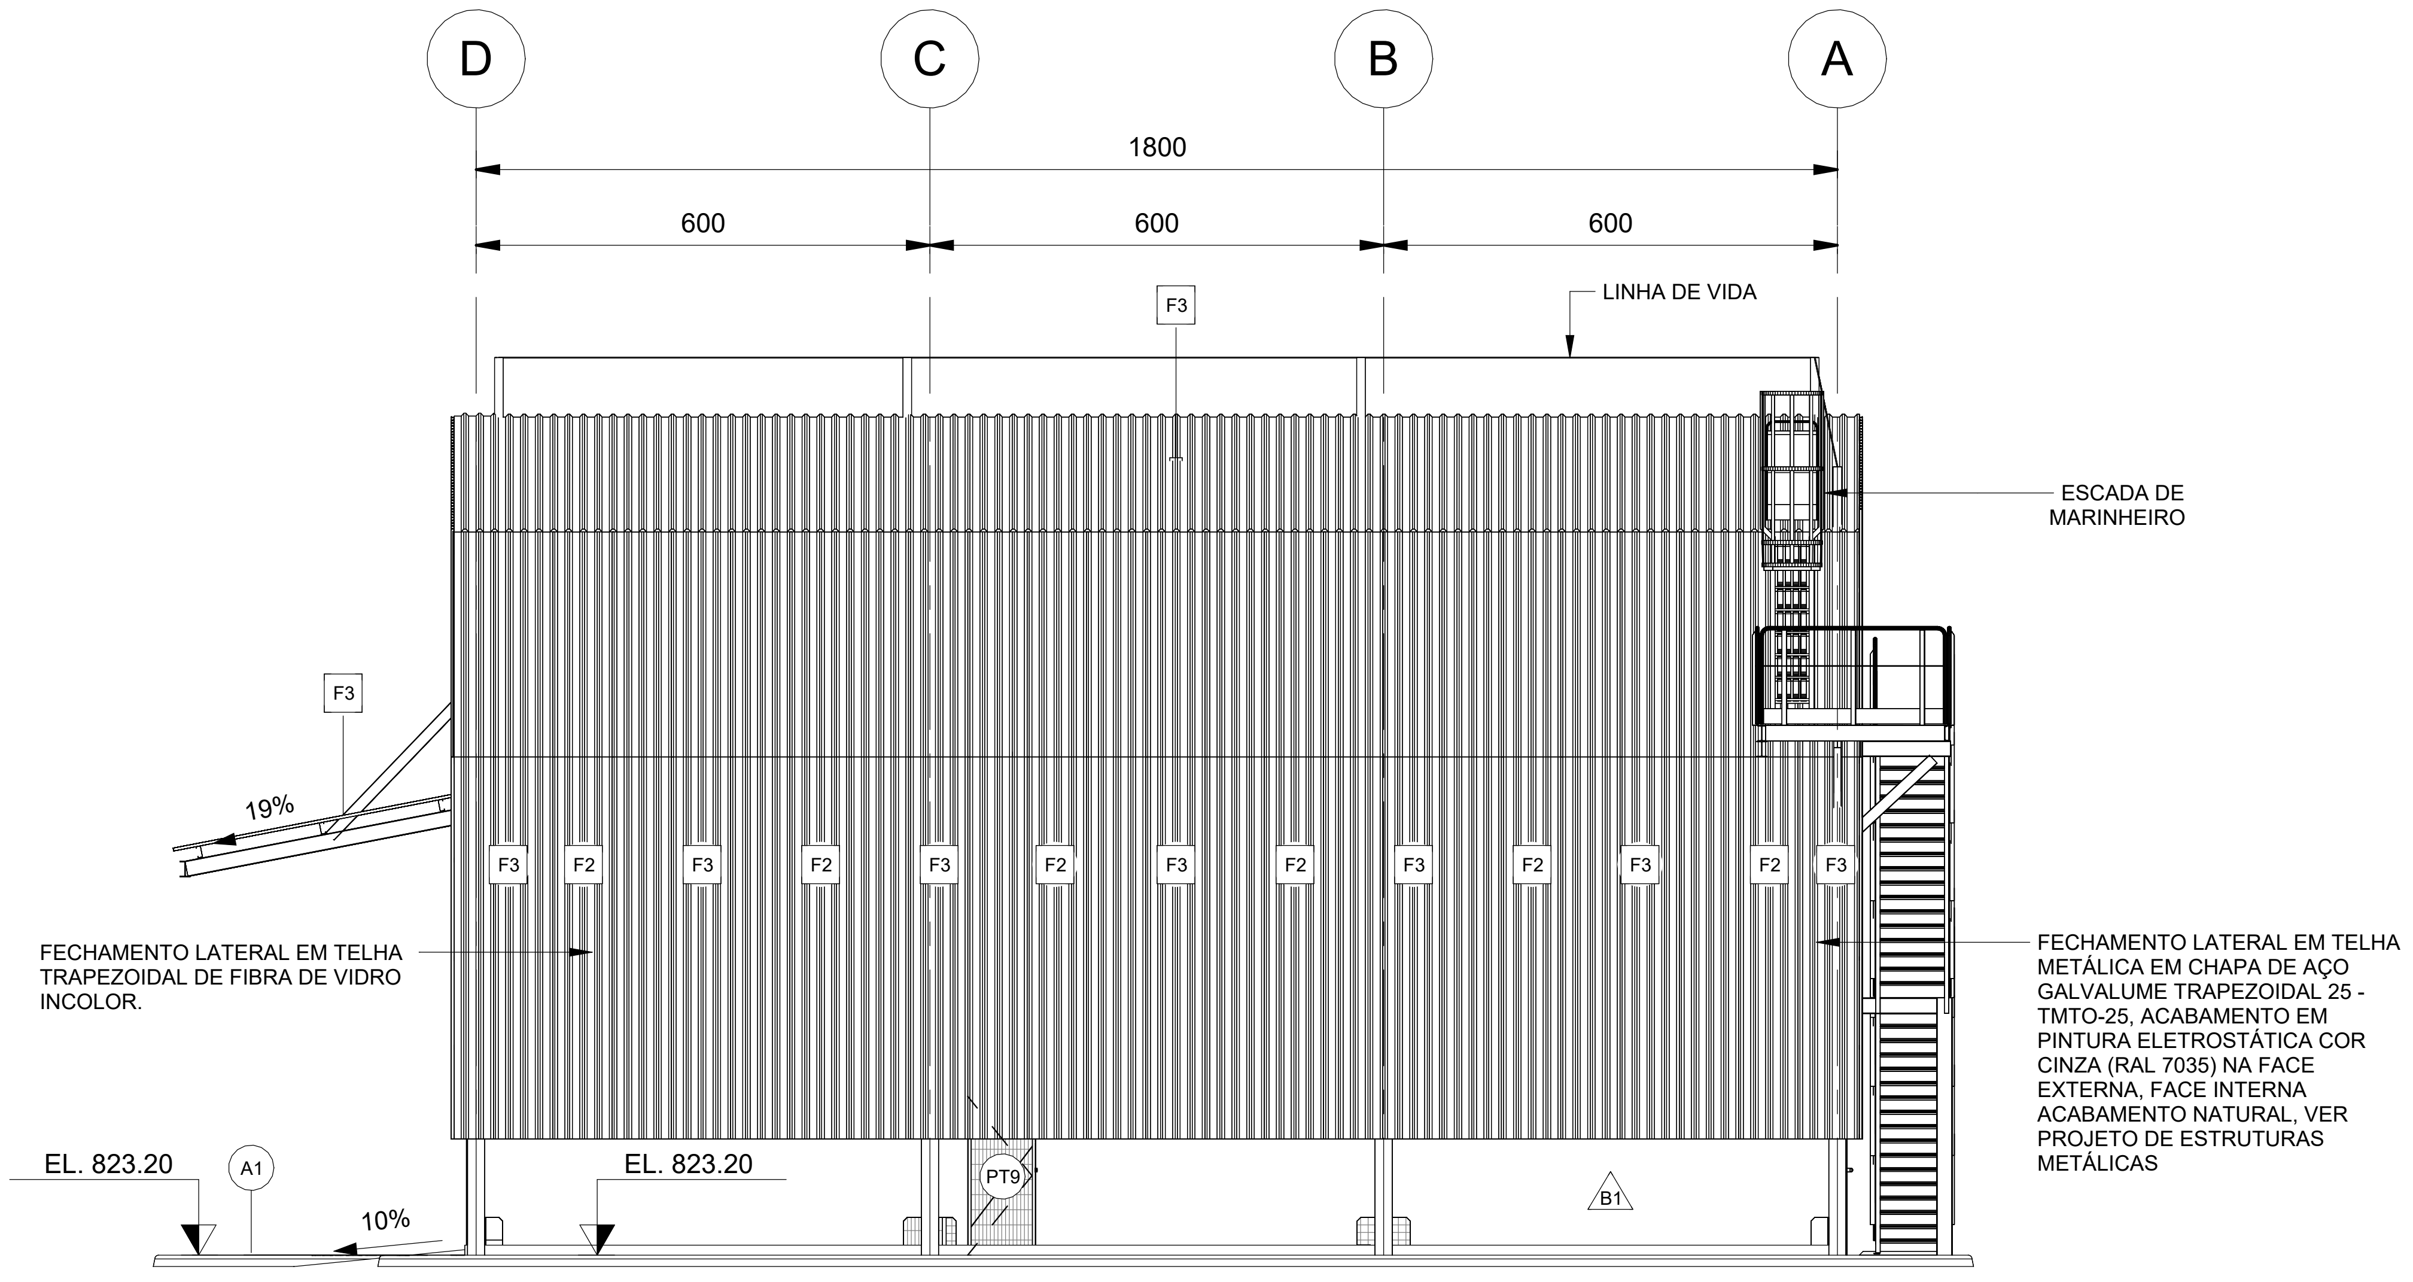
D
C
B
A
1800
600
600
600
F3
LINHA DE VIDA
ESCADA DE MARINHEIRO
F3
19%
F3 F2 F3 F2 F3 F2 F3 F2 F3 F2 F3 F2 F3
FECHAMENTO LATERAL EM TELHA TRAPEZOIDAL DE FIBRA DE VIDRO INCOLOR.
FECHAMENTO LATERAL EM TELHA METÁLICA EM CHAPA DE AÇO GALVALUME TRAPEZOIDAL 25 - TMTO-25, ACABAMENTO EM PINTURA ELETROSTÁTICA COR CINZA (RAL 7035) NA FACE EXTERNA, FACE INTERNA ACABAMENTO NATURAL, VER PROJETO DE ESTRUTURAS METÁLICAS
EL. 823.20
A1
10%
EL. 823.20
PT9
B1

ELEVAÇÃO 1

1 : 100

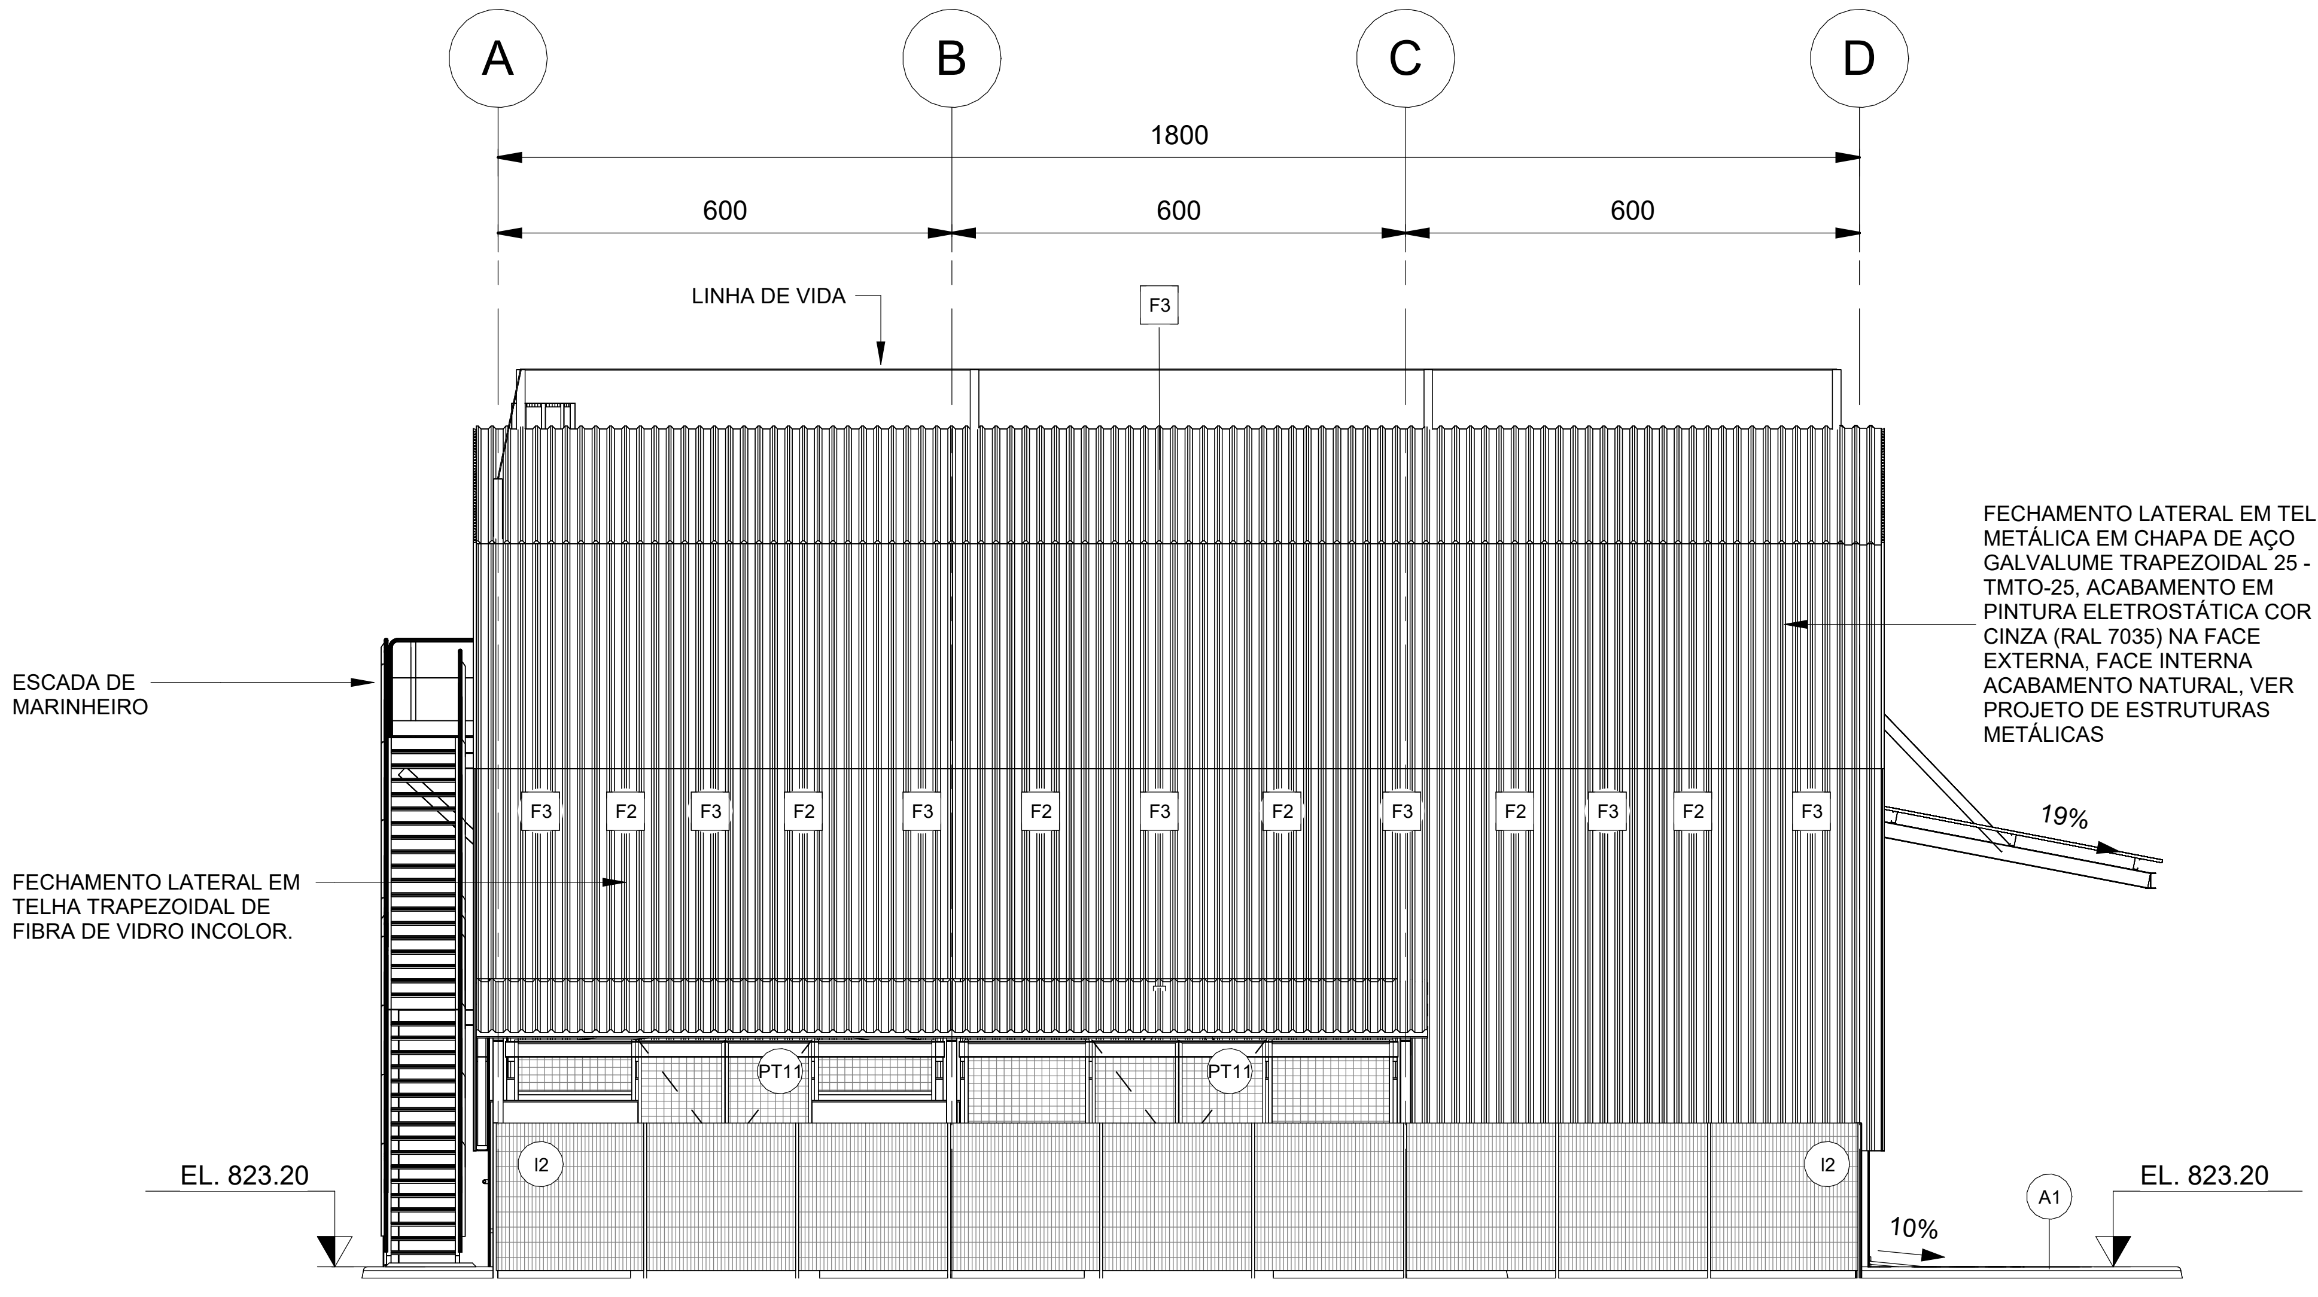
A
B
C
D
1800
600
600
600
LINHA DE VIDA
F3
FECHAMENTO LATERAL EM TELHA METÁLICA EM CHAPA DE AÇO GALVALUME TRAPEZOIDAL 25 - TMTO-25, ACABAMENTO EM PINTURA ELETROSTÁTICA COR CINZA (RAL 7035) NA FACE EXTERNA, FACE INTERNA ACABAMENTO NATURAL, VER PROJETO DE ESTRUTURAS METÁLICAS
ESCADA DE MARINHEIRO
F3 F2 F3 F2 F3 F2 F3 F2 F3 F2 F3 F2 F3
19%
FECHAMENTO LATERAL EM TELHA TRAPEZOIDAL DE FIBRA DE VIDRO INCOLOR.
PT11
PT11
I2
I2
EL. 823.20
10%
A1
EL. 823.20

ELEVAÇÃO 3

1 : 100

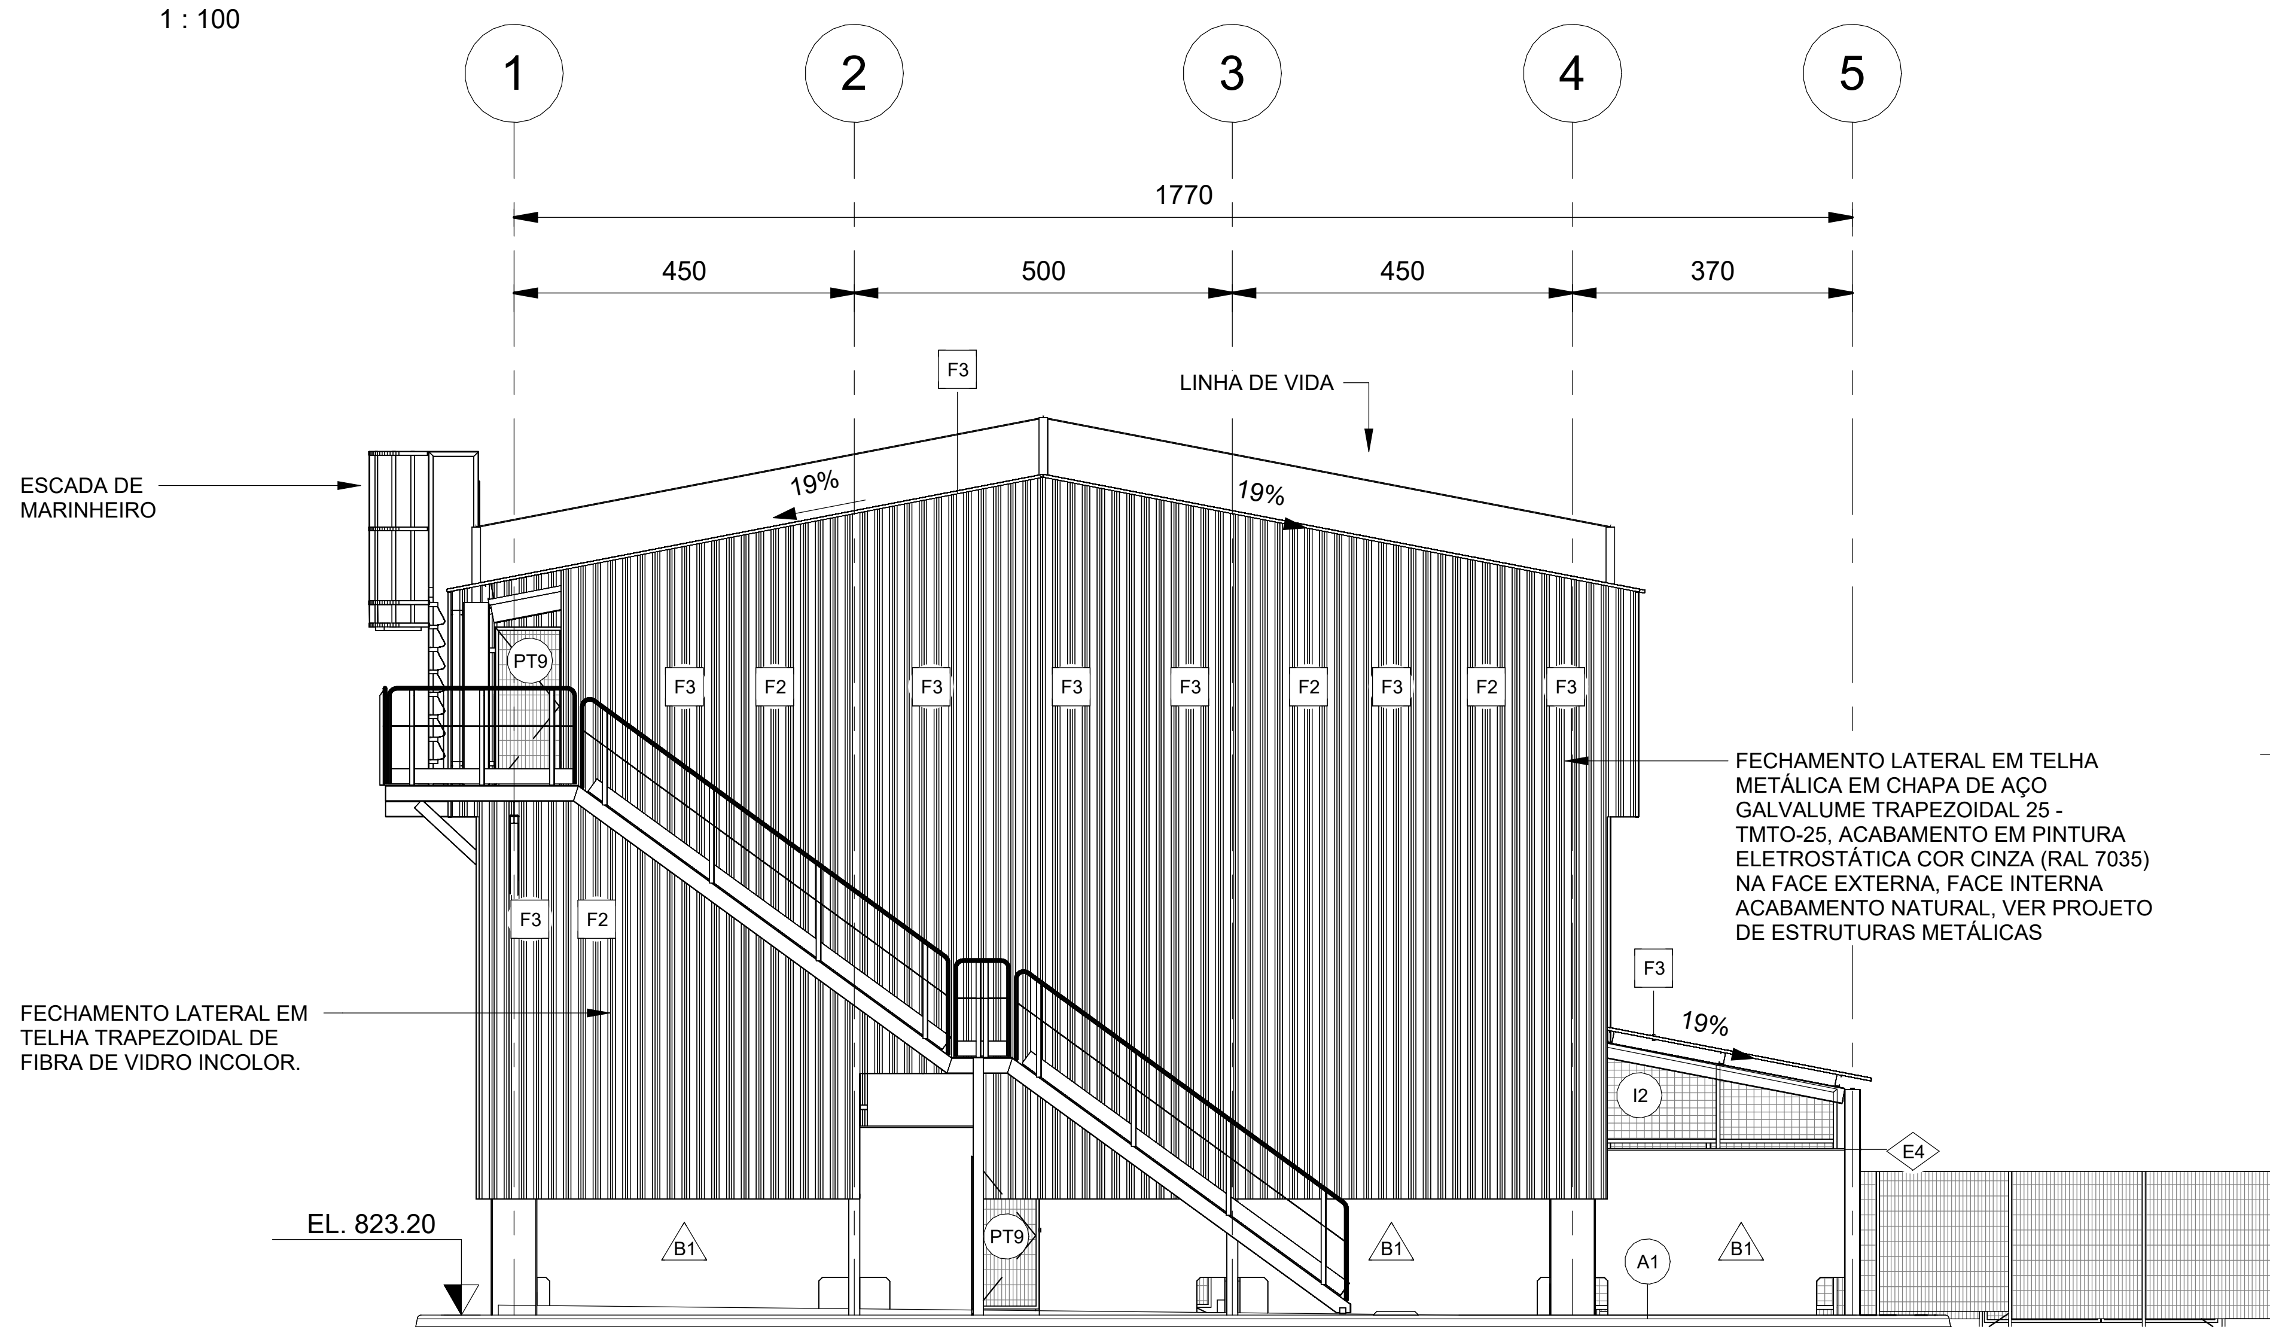
1
2
3
4
5
1770
450
500
450
370
F3
LINHA DE VIDA
ESCADA DE MARINHEIRO
19%
19%
PT9
F3 F2 F3 F3 F3 F2 F3 F2 F3
F3 F2
FECHAMENTO LATERAL EM TELHA METÁLICA EM CHAPA DE AÇO GALVALUME TRAPEZOIDAL 25 - TMTO-25, ACABAMENTO EM PINTURA ELETROSTÁTICA COR CINZA (RAL 7035) NA FACE EXTERNA, FACE INTERNA ACABAMENTO NATURAL, VER PROJETO DE ESTRUTURAS METÁLICAS
F3
19%
FECHAMENTO LATERAL EM TELHA TRAPEZOIDAL DE FIBRA DE VIDRO INCOLOR.
I2
E4
I2
EL. 823.20
B1
PT9
B1
A1
B1

ELEVAÇÃO 4

1 : 100

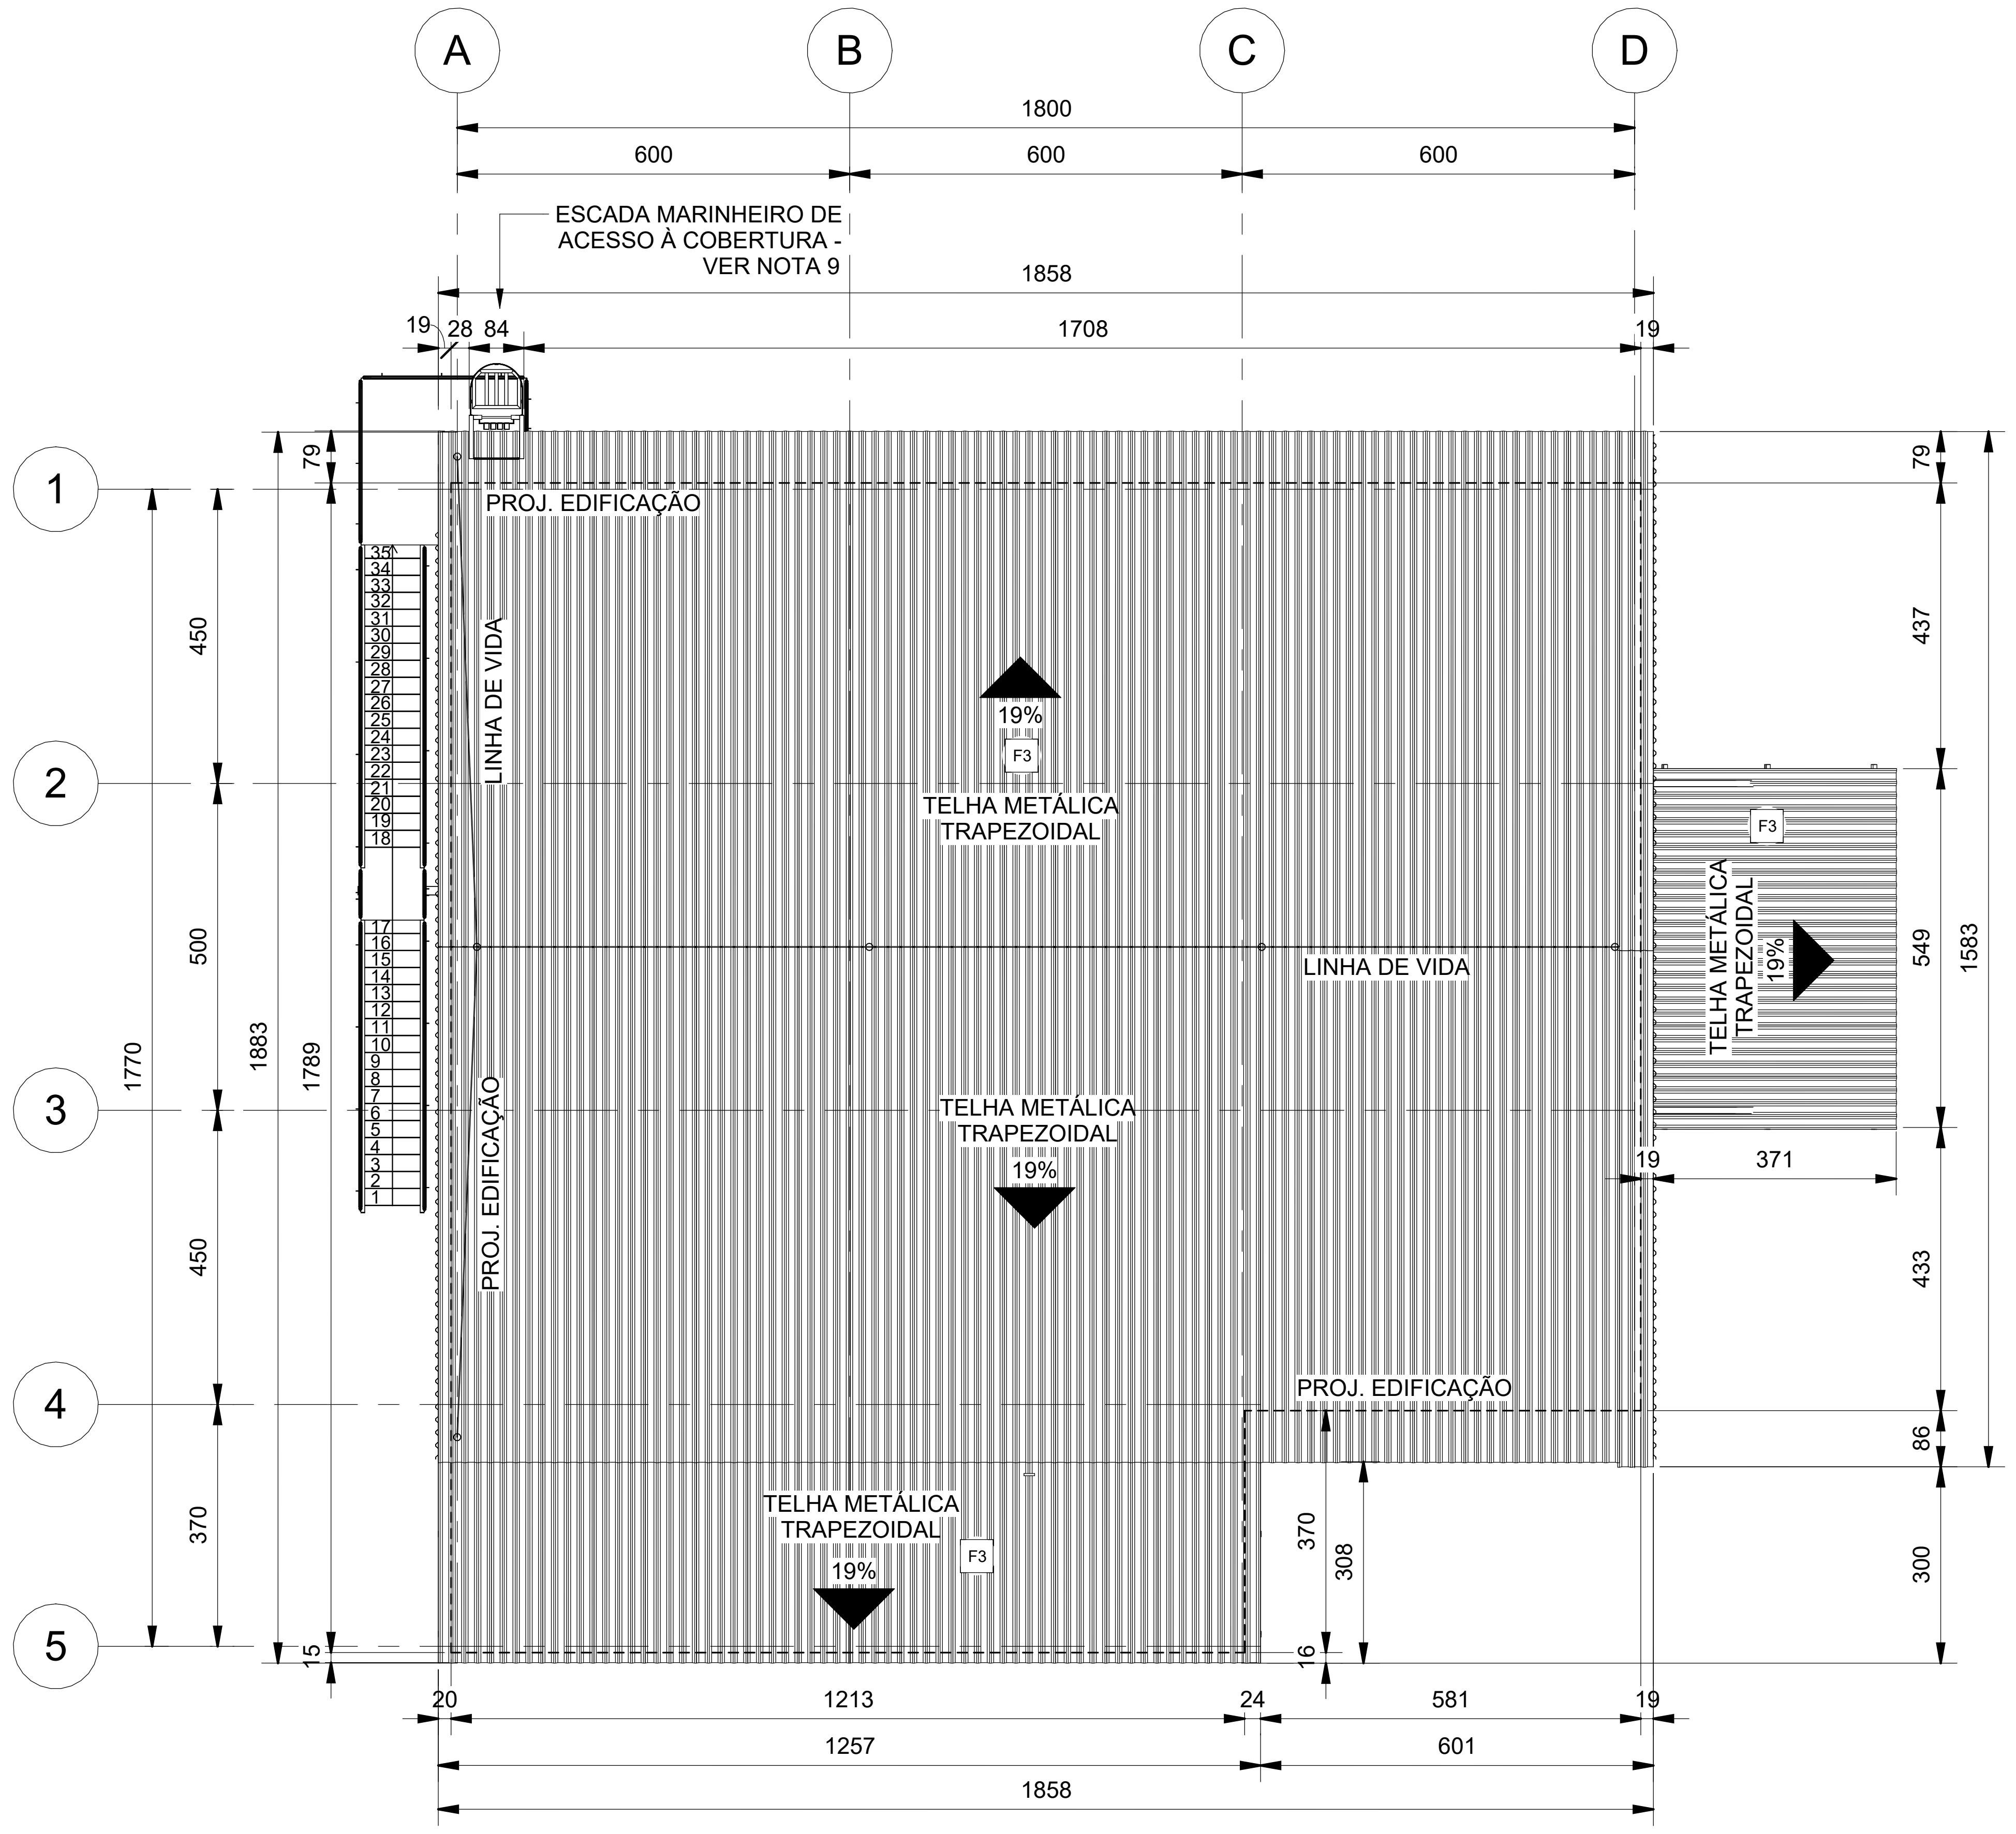

PLANTA DE COBERTURA

1 : 100

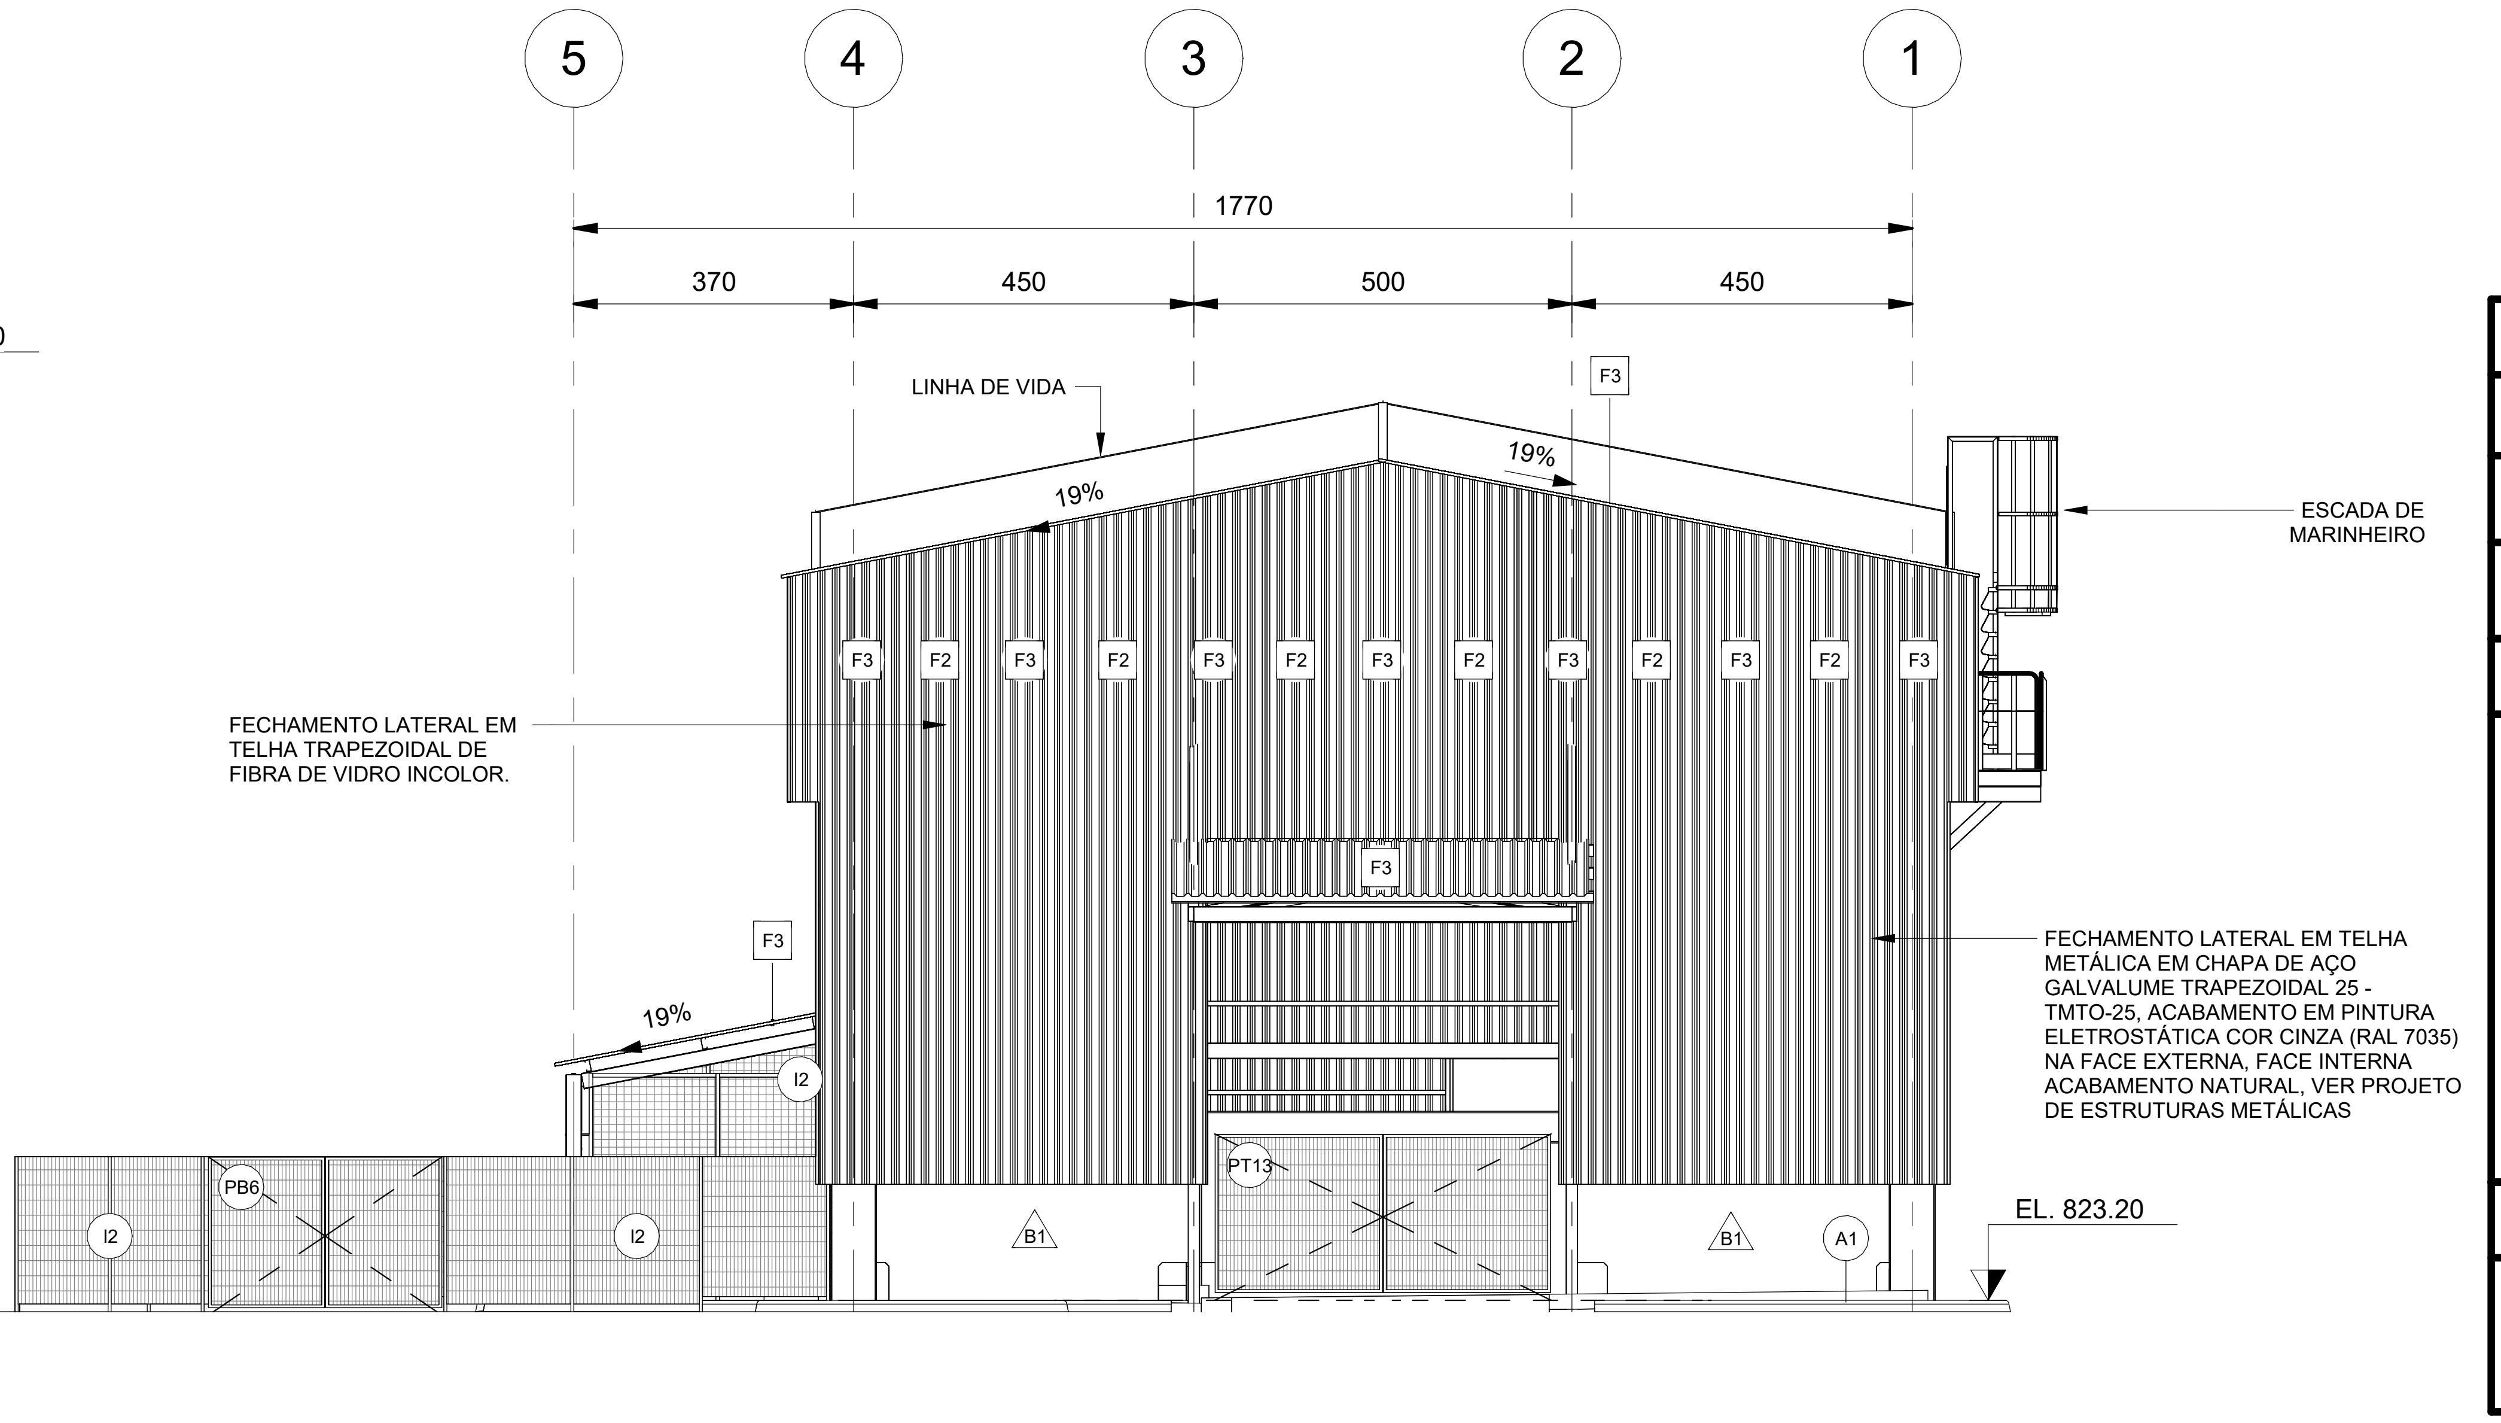
5
4
3
2
1
1770
370
450
500
450
F3
LINHA DE VIDA
19%
19%
ESCADA DE MARINHEIRO
F3 F2 F3 F2 F3 F2 F3 F2 F3 F2 F3 F2 F3
FECHAMENTO LATERAL EM TELHA TRAPEZOIDAL DE FIBRA DE VIDRO INCOLOR.
F3
FECHAMENTO LATERAL EM TELHA METÁLICA EM CHAPA DE AÇO GALVALUME TRAPEZOIDAL 25 - TMTO-25, ACABAMENTO EM PINTURA ELETROSTÁTICA COR CINZA (RAL 7035) NA FACE EXTERNA, FACE INTERNA ACABAMENTO NATURAL, VER PROJETO DE ESTRUTURAS METÁLICAS
19%
I2
PB6
I2
I2
PT13
B1
B1
A1
EL. 823.20

ELEVAÇÃO 2

1 : 100

QUADRO DE ESQUADRIAS

CÓD.	LARGURA (cm)	ALTURA (cm)	DESCRIÇÃO	QTD.
PORTAS				
PB6	300	210	PORTÃO DE GIRO, 2 FOLHAS, ESTRUTURA TUBULAR EM AÇO CARBONO DIÂM.=1 1/2", QUADRO FIXO COM TUBOS DIÂM.=1 '' E VEDAÇÃO EM TELA DE ARAME DE AÇO GALVANIZADO, MALHA 2 '' , FIO Nº 12 BWG E BARRA REDONDA ∅1/2'' . TRINCO DESLIZANTE TIPO FERROLHO PARA CADEADO. APLICAÇÃO DE PINTURA COR CINZA MÉDIO (RAL 7046), ACABAMENTO BRILHANTE.	1
PT9	90	210	PORTÃO DE GIRO, 1 FOLHA, ESTRUTURA TUBULAR EM AÇO CARBONO DIÂM.=1 1/2", QUADRO FIXO COM TUBOS DIÂM.=1 '' E VEDAÇÃO EM TELA DE ARAME DE AÇO GALVANIZADO, MALHA 2 '' , FIO Nº 12 BWG E BARRA REDONDA ∅1/2'' . TRINCO DESLIZANTE TIPO FERROLHO PARA CADEADO. APLICAÇÃO DE PINTURA COR CINZA MÉDIO (RAL 7046), ACABAMENTO BRILHANTE.	3
PT11	220	300	PORTÃO DE GIRO, 2 FOLHAS, ESTRUTURA TUBULAR EM AÇO CARBONO DIÂM.=1 1/2", QUADRO FIXO COM TUBOS DIÂM.=1 '' E VEDAÇÃO EM TELA DE ARAME DE AÇO GALVANIZADO, MALHA 2 '' , FIO Nº 12 BWG E BARRA REDONDA ∅1/2'' . TRINCO DESLIZANTE TIPO FERROLHO PARA CADEADO. APLICAÇÃO DE PINTURA COR CINZA MÉDIO (RAL 7046), ACABAMENTO BRILHANTE.	2
PT12	300	210	PORTÃO DE CORRER, 1 FOLHA, ESTRUTURA TUBULAR EM AÇO CARBONO DIÂM.=1 1/2", QUADRO FIXO COM TUBOS DIÂM.=1 '' E VEDAÇÃO EM TELA DE ARAME DE AÇO GALVANIZADO, MALHA 2 '' , FIO Nº 12 BWG E BARRA REDONDA ∅1/2'' . TRINCO DESLIZANTE TIPO FERROLHO PARA CADEADO. APLICAÇÃO DE PINTURA COR CINZA MÉDIO (RAL 7046), ACABAMENTO BRILHANTE.	1
PT13	435	220	PORTÃO DE GIRO, 2 FOLHAS, ESTRUTURA TUBULAR EM AÇO CARBONO DIÂM.=1 1/2", QUADRO FIXO COM TUBOS DIÂM.=1 '' E VEDAÇÃO EM TELA DE ARAME DE AÇO GALVANIZADO, MALHA 2 '' , FIO Nº 12 BWG E BARRA REDONDA ∅1/2'' . TRINCO DESLIZANTE TIPO FERROLHO PARA CADEADO. APLICAÇÃO DE PINTURA COR CINZA MÉDIO (RAL 7046), ACABAMENTO BRILHANTE.	1
PT14	90	210	PORTÃO DE GIRO, 1 FOLHA, ESTRUTURA TUBULAR EM AÇO CARBONO DIÂM.=1 1/2", QUADRO FIXO COM TUBOS DIÂM.=1 '' E VEDAÇÃO EM TELA DE ARAME DE AÇO GALVANIZADO, MALHA 2 '' , FIO Nº 12 BWG E BARRA REDONDA ∅1/2'' . TRINCO DESLIZANTE TIPO FERROLHO PARA CADEADO. APLICAÇÃO DE PINTURA COR CINZA MÉDIO (RAL 7046), ACABAMENTO BRILHANTE.	1

QUADRO ESPECIFICAÇÕES DE ACABAMENTOS

CÓDIGO	DESCRIÇÃO
○	PISOS
A1	PISO EM CONCRETO DESEMPENADO COM JUNTA SECA A CADA 1,20cm, ACABAMENTO VASSOURADO, ESP. 10cm
A6	PISO EM CONCRETO ARMADO, VER PROJETO DE CIVIL/CONCRETO
△	PAREDES
B1	ALVENARIA EM BLOCO DE CONCRETO REVESTIDA COM CHAPISCO, EMBOÇO E REBOCO E SELADOR ACRÍLICO, APLICAÇÃO DE DUAS DEMÃOS DE TINTA LÁTEX ACRÍLICA, ACABAMENTO ACETINADO, COR TERRACOTA, REF.: COR TERRACOTA (CÓD. R118) - SUVINIL OU SIMILAR
B2	ALVENARIA EM BLOCO DE CONCRETO REVESTIDA COM CHAPISCO, EMBOÇO E REBOCO E SELADOR ACRÍLICO, APLICAÇÃO DE DUAS DEMÃOS DE TINTA LÁTEX ACRÍLICA, ACABAMENTO ACETINADO, COR CINZA CLARO (RAL 7035) , REF.: SUVINIL OU SIMILAR
◇	SOLEIRAS, RODAPÉS E PEITORIS
E4	PEITORIL EM CONCRETO PRÉ-MOLDADO, ACABAMENTO LISO, COM PINGADEIRA, ESPESSURA 3cm, ASSENTADO COM ARGAMASSA COLANTE
E6	RODAPÉ EM CONCRETO PRÉ-MOLDADO, ACABAMENTO LISO, ESPESSURA 3cm, H=10cm, ASSENTADO COM ARGAMASSA COLANTE
○	CERCAMENTOS
I2	ALAMBRADO EM ESTRUTURA TUBULAR EM AÇO CARBONO DIÂM.=2", QUADRO FIXO COM TUBOS DIÂM.=1 '' E VEDAÇÃO EM TELA DE ARAME DE AÇO GALVANIZADO, MALHA QUADRADA 50mm (2 ''), FIO Nº 12 BWG E BARRA REDONDA ∅1/2''. APLICAÇÃO DE PINTURA ELETROSTÁTICA COR CINZA MÉDIO (RAL 7046), ACABAMENTO BRILHANTE
□	COBERTURAS
F2	TELHA TRAPEZOIDAL DE FIBRA DE VIDRO INCOLOR, VER PROJETO DE ESTRUTURAS METÁLICAS
F3	TELHA METÁLICA EM CHAPA DE AÇO GALVALUME TRAPEZOIDAL, H=40mm, ESPESSURA=65mm, ACABAMENTO EM PINTURA ESMALTE COR CINZA FACE EXTERNA, FACE INTERNA ACABAMENTO NATURAL, VER PROJETO DE ESTRUTURAS METÁLICAS

CODIFICAÇÃO AWP – ADVANCED WORK PACKAGING

CWA	CÓDIGOS: CWA 001 - PLATÔ DOS PRÉDIOS OPERACIONAIS
CWP	CÓDIGOS: CWP 007 - OFICINA AVANÇADA G1342ED08-CWA 001-G-MT-0001.007-CWP 007
EWP	CÓDIGOS: G1342ED08-CWA 001-G-MT-0001.007-EWP 007

NOTAS

1- DIMENSÕES EM CENTÍMETROS, ELEVAÇÕES E COORDENADAS EM METRO, SALVO INDICAÇÃO EM CONTRÁRIO;
2 - AS ELEVAÇÕES APRESENTADAS EM PROJETO CORRESPONDEM AO NÍVEL DO PISO ACABADO;
3 - PARA ESPECIFICAÇÕES DETALHADAS DOS MATERIAIS E ACABAMENTOS, VER CADERNO DE ESPECIFICAÇÕES DA SAMARCO (DOCUMENTO Nº T000000-G-6NT004);
4 - PARA AS PAREDES EXTERNAS E INTERNAS DA OFICINA SERÃO UTILIZADOS BLOCOS DE CONCRETO COM ESPESSURA DE 14cm.
5 - A ELEVAÇÃO 0,00 NO PROJETO CORRESPONDE À COTA +823,00 DO PROJETO DE INFRAESTRUTURA (DOCUMENTO SAMARCO Nº G134448-O-1000105).
6 - O ESCOPO DA DISCIPLINA DE ARQUITETURA NA OFICINA AVANÇADA SE LIMITA AS DEFINIÇÕES DOS CERCAMENTOS, ALAMBRADOS, ESQUADRIAS, ALVENARIAS E ACABAMENTOS. A DISPOSIÇÃO DOS AMBIENTES INTERNOS, O LAYOUT, E OS ACESSOS FORAM DEFINIDOS PELA MECÂNICA.
7 - AS ALVENARIAS DE DIVISÃO ENTRE O DEPÓSITO DE TAMBORES E O COMPRESSOR, E ENTRE O DEPÓSITO E A OFICINA DEVERÃO POSSUIR PROPRIEDADES CORTA-FOGO, CONFORME IT-06 DO CBMMG. DESTA FORMA, DEVERÃO SER EXECUTADAS COM BLOCO DE CONCRETO DE 14cm DE ESPESSURA, COM UMA CAMADA DE CHAPISCO E EMBOÇO DE NO MÍNIMO 1,5cm.
8 - PARA LAYOUT DA OFICINA AVANÇADA, VER DOCUMENTO MECÂNICA NºG134211-M-100039.
9 - A ESCADA DE MARINHEIRO PARA ACESSO À COBERTURA DEVERÁ SEGUIR AS PREMISSAS DOCUMENTO DE SEGURANÇA DA SAMARCO Nº T000002-S-2PS004;

DESENHOS DE REFERÊNCIA

1 - IMPLANTAÇÃO DA ARQUITETURA - DOC. Nº G134140-C-800038
2 - DESENHOS COMPLEMENTARES G134240-C-800030 / G134240-C-800031 / G134240-C-8000XX / G134240-C-8000XX
3 - DETALHAMENTO DE ESQUADRIAS - DOC. Nº G130000-C-800001 / G130000-C-800002 / G130000-C-800003 / G130000-C-800004

ESPESSURA DE LINHAS DA SAMARCO
1 – RED – 0,10mm
2 – YELLOW – 0,5mm
3 – GREEN – 0,20mm
4 – CYAN – 0,30mm
5 – BLUE – 0,15mm
6 – MAGENTA – 0,60mm
7 – WHITE – 0,40mm
8 – CINZA – 0,80mm

ESPESSURA DE LINHAS EXTRAS ADOTADAS NESTE DESENHO SAMARCO
17 18 19
20 21 22
23 24 25

A1

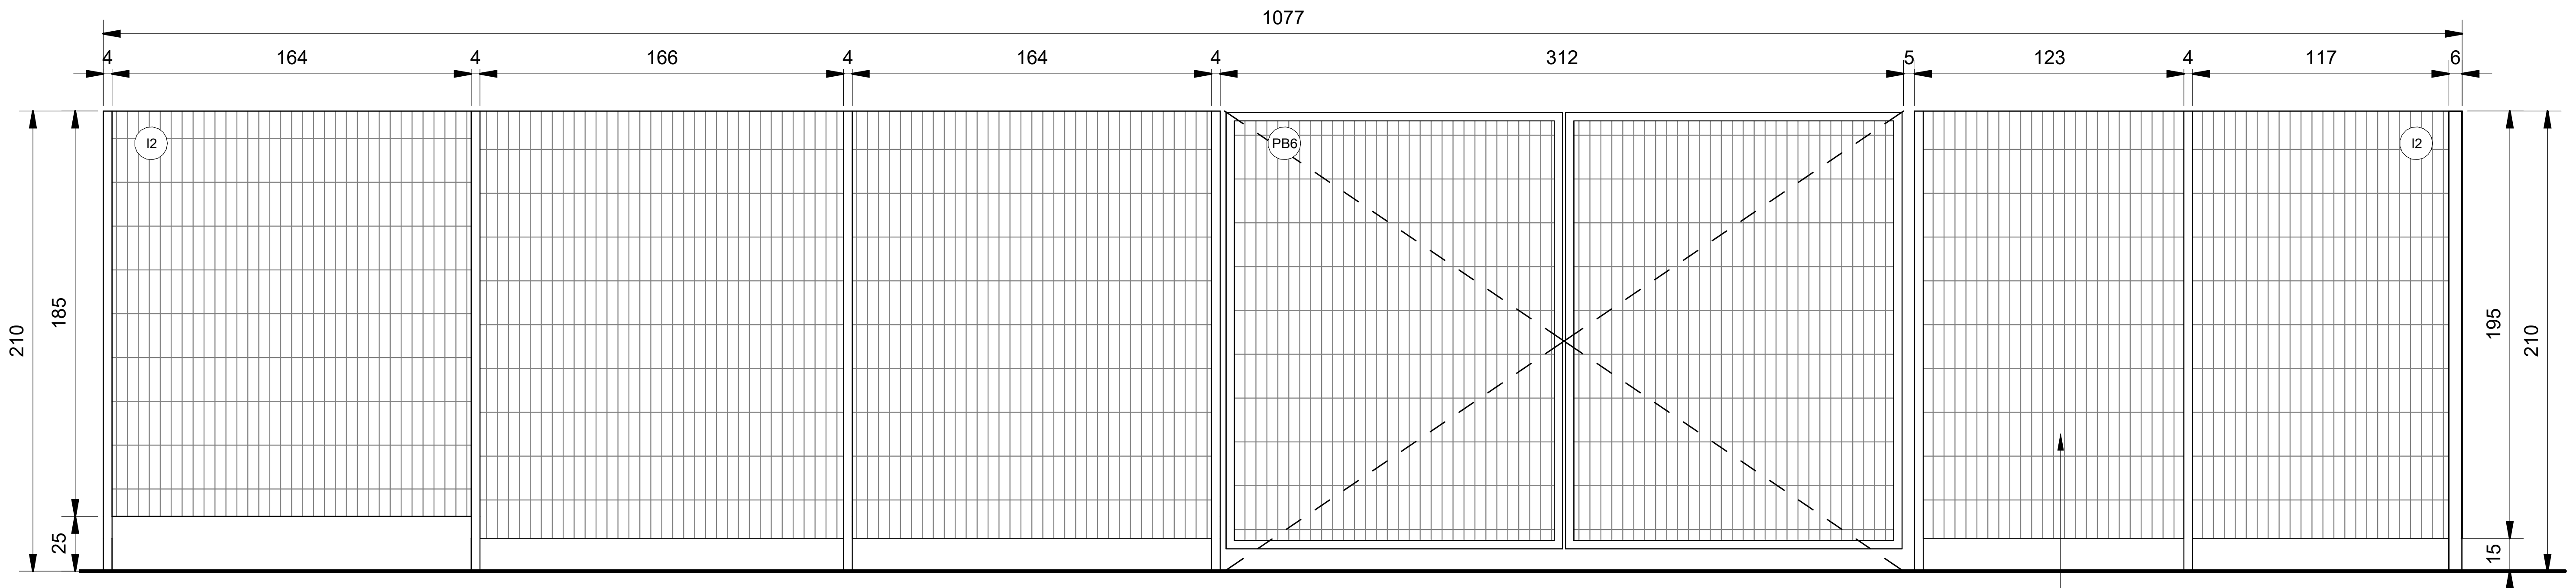
1077
164
4
166
4
164
4
312
5
123
4
117
6
I2
PB6
I2
210
185
25
195
210
15
ALAMBRADO EM ESTRUTURA TUBULAR EM AÇO CARBONO DIÂM.=2", QUADRO FIXO COM TUBOS DIÂM.=1'' E VEDAÇÃO EM TELA DE ARAME DE AÇO GALVANIZADO, MALHA QUADRADA 50mm (2''), FIO Nº 12 BWG E BARRA REDONDA ∅1/2''. APLICAÇÃO DE PINTURA ELETROSTÁTICA COR CINZA MÉDIO (RAL 7046), ACABAMENTO BRILHANTE

CERCAMENTO - VISTA 03

1 : 25

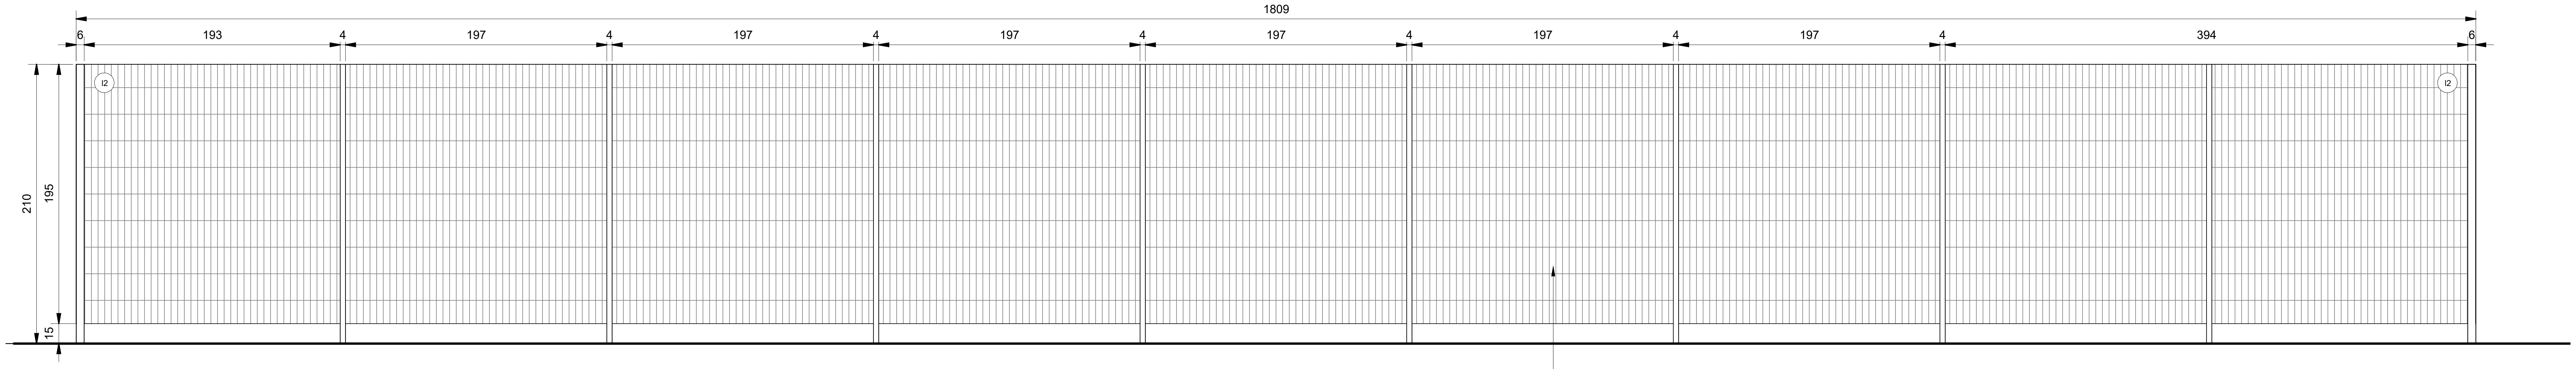
1809
6
193
4
197
4
197
4
197
4
197
4
197
4
197
4
394
6
I2
I2
210
195
15
ALAMBRADO EM ESTRUTURA TUBULAR EM AÇO CARBONO DIÂM.=2", QUADRO FIXO COM TUBOS DIÂM.=1'' E VEDAÇÃO EM TELA DE ARAME DE AÇO GALVANIZADO, MALHA QUADRADA 50mm (2''), FIO Nº 12 BWG E BARRA REDONDA ∅1/2''. APLICAÇÃO DE PINTURA ELETROSTÁTICA COR CINZA MÉDIO (RAL 7046), ACABAMENTO BRILHANTE

CERCAMENTO - VISTA 02

1 : 25

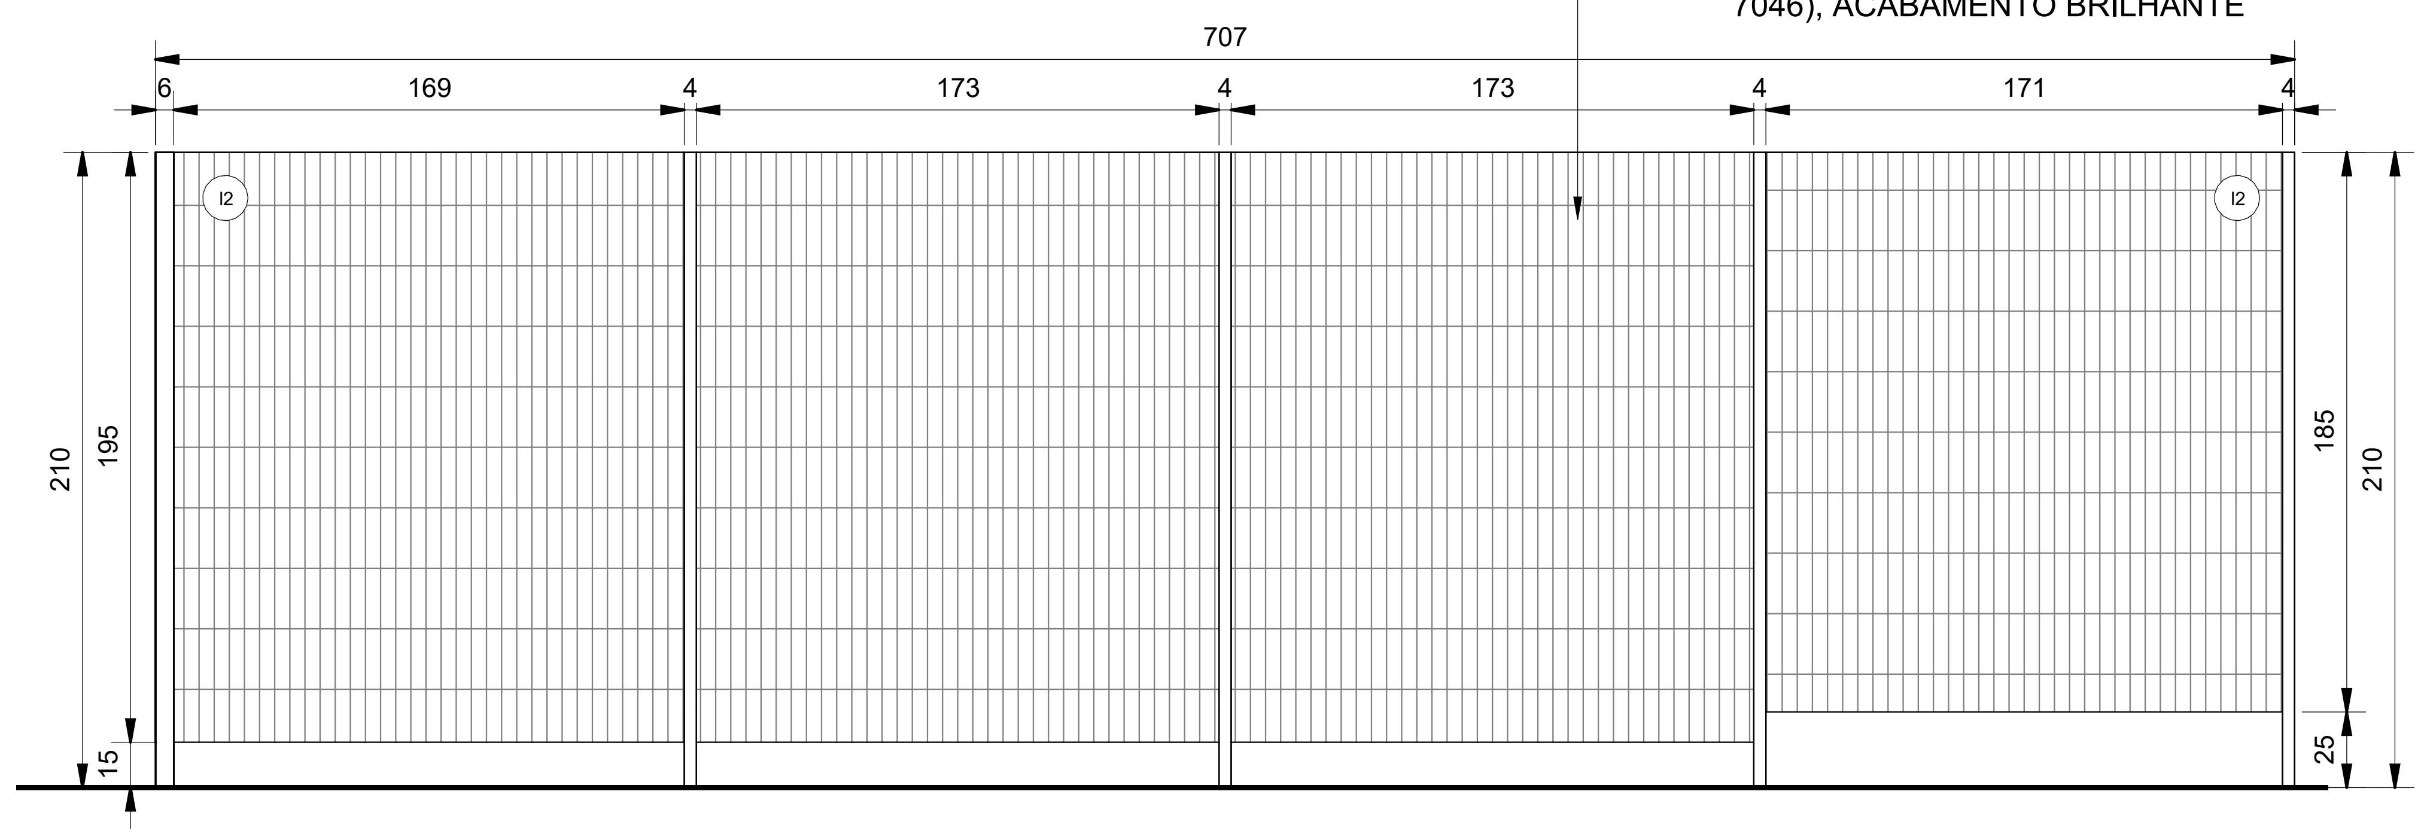
ALAMBRADO EM ESTRUTURA TUBULAR EM AÇO CARBONO DIÂM.=2", QUADRO FIXO COM TUBOS DIÂM.=1'' E VEDAÇÃO EM TELA DE ARAME DE AÇO GALVANIZADO, MALHA QUADRADA 50mm (2''), FIO Nº 12 BWG E BARRA REDONDA ∅1/2''. APLICAÇÃO DE PINTURA ELETROSTÁTICA COR CINZA MÉDIO (RAL 7046), ACABAMENTO BRILHANTE
707
6
169
4
173
4
173
4
171
4
I2
I2
210
195
15
185
210
25

CERCAMENTO - VISTA 01

1 : 25

QUADRO DE ESQUADRIAS

CÓD.	LARGURA (cm)	ALTURA (cm)	DESCRIÇÃO	QTD.
PORTAS				
PB6	300	210	PORTÃO DE GIRO, 2 FOLHAS, ESTRUTURA TUBULAR EM AÇO CARBONO DIÂM.=1 1/2", QUADRO FIXO COM TUBOS DIÂM.=1'' E VEDAÇÃO EM TELA DE ARAME DE AÇO GALVANIZADO, MALHA 2'' , FIO Nº 12 BWG E BARRA REDONDA ∅1/2'' . TRINCO DESLIZANTE TIPO FERROLHO PARA CADEADO. APLICAÇÃO DE PINTURA COR CINZA MÉDIO (RAL 7046), ACABAMENTO BRILHANTE.	1

QUADRO ESPECIFICAÇÕES DE ACABAMENTOS

CÓDIGO	DESCRIÇÃO
○	PISOS
A1	PISO EM CONCRETO DESEMPENADO COM JUNTA SECA A CADA 1,20cm, ACABAMENTO VASSOURADO, ESP. 10cm
A6	PISO EM CONCRETO ARMADO, VER PROJETO DE CIVIL/CONCRETO
△	PAREDES
B1	ALVENARIA EM BLOCO DE CONCRETO REVESTIDA COM CHAPISCO, EMBOÇO E REBOCO E SELADOR ACRÍLICO, APLICAÇÃO DE DUAS DEMÃOS DE TINTA LÁTEX ACRÍLICA, ACABAMENTO ACETINADO, COR TERRACOTA, REF.: COR TERRACOTA (CÓD. R118) - SUVINIL OU SIMILAR
B2	ALVENARIA EM BLOCO DE CONCRETO REVESTIDA COM CHAPISCO, EMBOÇO E REBOCO E SELADOR ACRÍLICO, APLICAÇÃO DE DUAS DEMÃOS DE TINTA LÁTEX ACRÍLICA, ACABAMENTO ACETINADO, COR CINZA CLARO (RAL 7035) , REF.: SUVINIL OU SIMILAR
◇	SOLEIRAS, RODAPÉS E PEITORIS
E4	PEITORIL EM CONCRETO PRÉ-MOLDADO, ACABAMENTO LISO, COM PINGADEIRA, ESPESSURA 3cm, ASSENTADO COM ARGAMASSA COLANTE
E6	RODAPÉ EM CONCRETO PRÉ-MOLDADO, ACABAMENTO LISO, ESPESSURA 3cm, H=10cm, ASSENTADO COM ARGAMASSA COLANTE
○	CERCAMENTOS
I2	ALAMBRADO EM ESTRUTURA TUBULAR EM AÇO CARBONO DIÂM.=2", QUADRO FIXO COM TUBOS DIÂM.=1'' E VEDAÇÃO EM TELA DE ARAME DE AÇO GALVANIZADO, MALHA QUADRADA 50mm (2''), FIO Nº 12 BWG E BARRA REDONDA ∅1/2''. APLICAÇÃO DE PINTURA ELETROSTÁTICA COR CINZA MÉDIO (RAL 7046), ACABAMENTO BRILHANTE
□	COBERTURAS
F2	TELHA TRAPEZOIDAL DE FIBRA DE VIDRO INCOLOR, VER PROJETO DE ESTRUTURAS METÁLICAS
F3	TELHA METÁLICA EM CHAPA DE AÇO GALVALUME TRAPEZOIDAL, H=40mm, ESPESSURA=65mm, ACABAMENTO EM PINTURA ESMALTE COR CINZA FACE EXTERNA, FACE INTERNA ACABAMENTO NATURAL, VER PROJETO DE ESTRUTURAS METÁLICAS

CODIFICAÇÃO AWP – ADVANCED WORK PACKAGING

CWA	CÓDIGOS:	CWA 001 - PLATÔ DOS PRÉDIOS OPERACIONAIS
CWP	CÓDIGOS:	CWP 007 - OFICINA AVANÇADA G1342ED08-CWA 001-G-MT-0001.007-CWP 007
EWP	CÓDIGOS:	G1342ED08-CWA 001-G-MT-0001.007-EWP 007

NOTAS

1- DIMENSÕES EM CENTÍMETROS, ELEVAÇÕES E COORDENADAS EM METRO, SALVO INDICAÇÃO EM CONTRÁRIO;
2 - AS ELEVAÇÕES APRESENTADAS EM PROJETO CORRESPONDEM AO NÍVEL DO PISO ACABADO;
3 - PARA ESPECIFICAÇÕES DETALHADAS DOS MATERIAIS E ACABAMENTOS, VER CADERNO DE ESPECIFICAÇÕES DA SAMARCO (DOCUMENTO Nº T000000-G-6NT004);
4 - PARA AS PAREDES EXTERNAS E INTERNAS DA OFICINA SERÃO UTILIZADOS BLOCOS DE CONCRETO COM ESPESSURA DE 14cm.
5 - A ELEVAÇÃO 0,00 NO PROJETO CORRESPONDE À COTA +823,00 DO PROJETO DE INFRAESTRUTURA (DOCUMENTO SAMARCO Nº G134448-O-1000105).
6 - O ESCOPO DA DISCIPLINA DE ARQUITETURA NA OFICINA AVANÇADA SE LIMITA AS DEFINIÇÕES DOS CERCAMENTOS, ALAMBRADOS, ESQUADRIAS, ALVENARIAS E ACABAMENTOS. A DISPOSIÇÃO DOS AMBIENTES INTERNOS, O LAYOUT, E OS ACESSOS FORAM DEFINIDOS PELA MECÂNICA.
7 - AS ALVENARIAS DE DIVISÃO ENTRE O DEPÓSITO DE TAMBORES E O COMPRESSOR, E ENTRE O DEPÓSITO E A OFICINA DEVERÃO POSSUIR PROPRIEDADES CORTA-FOGO, CONFORME IT-06 DO CBMMG. DESTA FORMA, DEVERÃO SER EXECUTADAS COM BLOCO DE CONCRETO DE 14cm DE ESPESSURA, COM UMA CAMADA DE CHAPISCO E EMBOÇO DE NO MÍNIMO 1,5cm.
8 - PARA LAYOUT DA OFICINA AVANÇADA, VER DOCUMENTO MECÂNICA NºG134211-M-100039.
9 - A ESCADA DE MARINHEIRO PARA ACESSO À COBERTURA DEVERÁ SEGUIR AS PREMISSAS DOCUMENTO DE SEGURANÇA DA SAMARCO Nº T000002-S-2PS004;

DESENHOS DE REFERÊNCIA

1 - IMPLANTAÇÃO DA ARQUITETURA - DOC. Nº G134140-C-800038
2 - DESENHOS COMPLEMENTARES G134240-C-800030 / G134240-C-800031 / G134240-C-800032 / G134240-C-8000XX
3 - DETALHAMENTO DE ESQUADRIAS - DOC. Nº G130000-C-800001 / G130000-C-800002 / G130000-C-800003 / G130000-C-800004

ESPESSURA DE LINHAS DA SAMARCO
1 – RED – 0,10mm
2 – YELLOW – 0,5mm
3 – GREEN – 0,20mm
4 – CYAN – 0,30mm
5 – BLUE – 0,15mm
6 – MAGENTA – 0,60mm
7 – WHITE – 0,40mm
8 – CINZA – 0,80mm

ESPESSURA DE LINHAS EXTRAS ADOTADAS NESTE DESENHO SAMARCO
17 18 19
20 21 22
23 24 25

A1

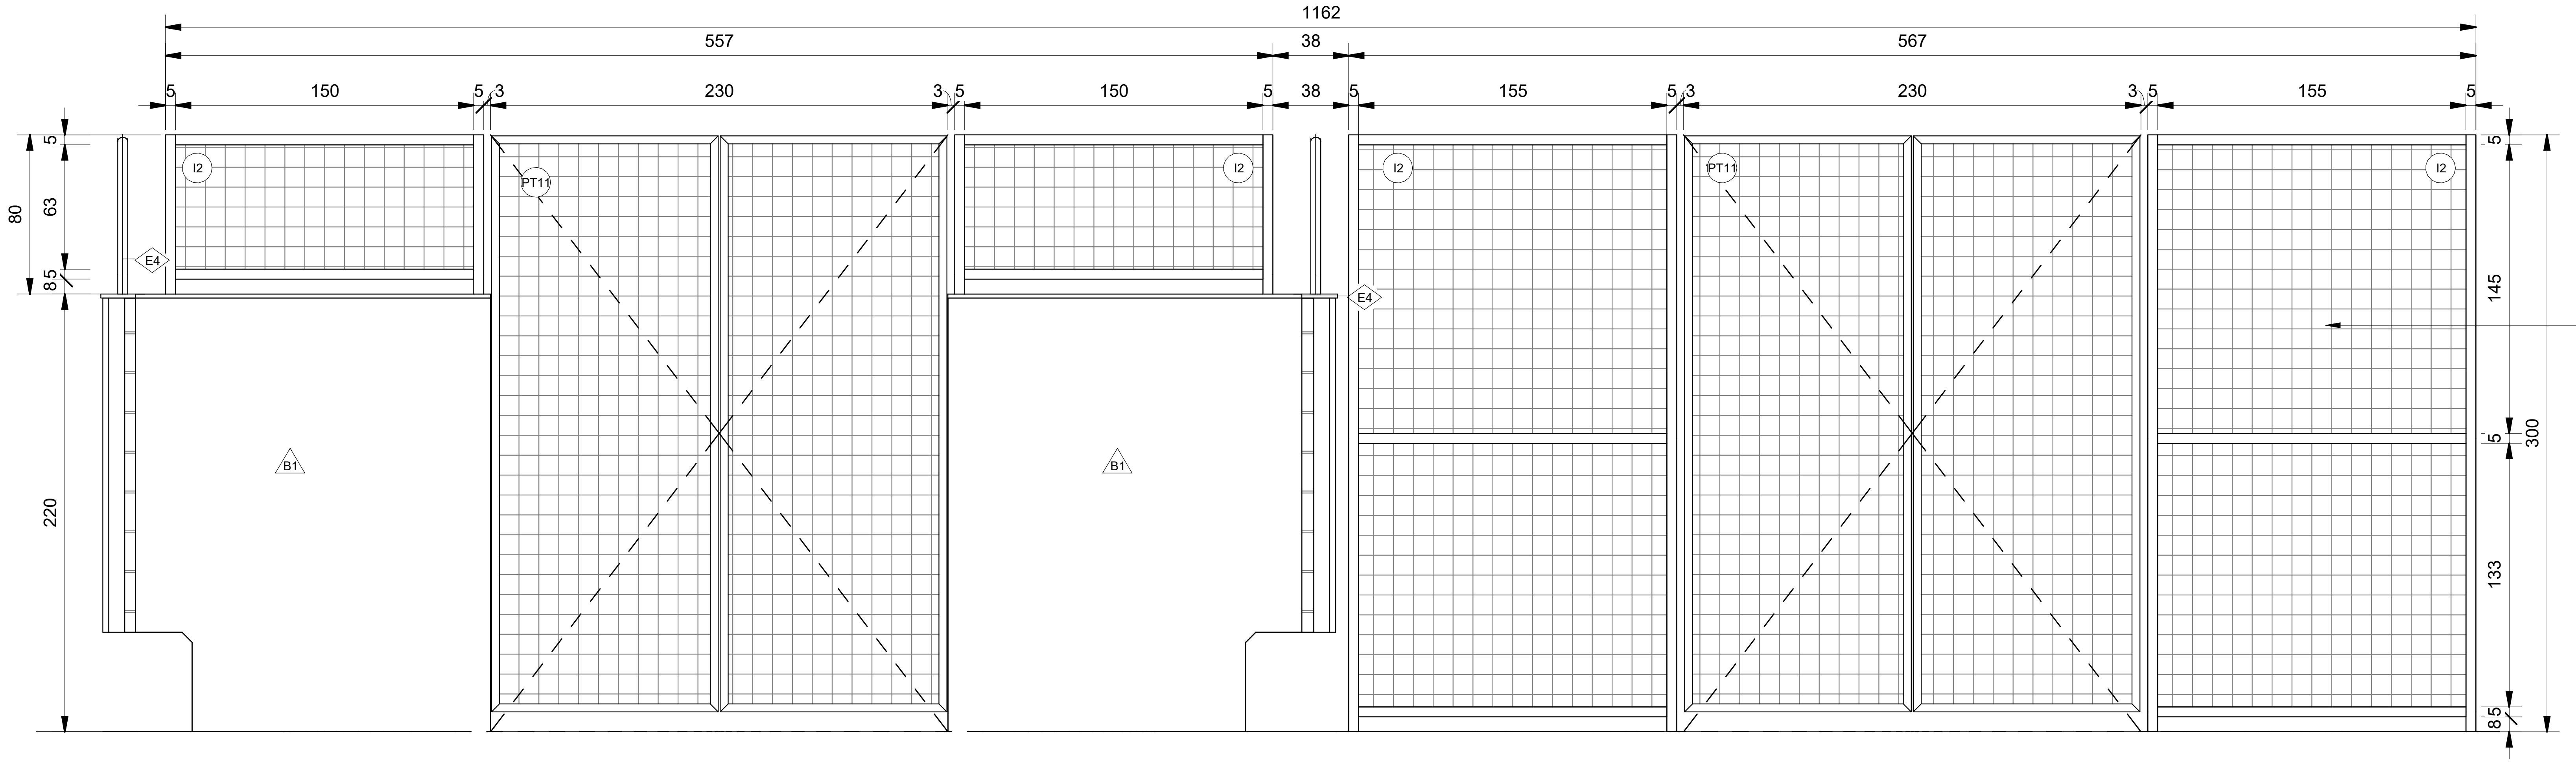

ALAMBRADO EM ESTRUTURA TUBULAR EM AÇO CARBONO DIÂM.=2", QUADRO FIXO COM TUBOS DIÂM.=1'' E VEDAÇÃO EM TELA DE ARAME DE AÇO GALVANIZADO, MALHA QUADRADA 50mm (2''), FIO Nº 12 BWG E BARRA REDONDA ∅1/2''. APLICAÇÃO DE PINTURA ELETROSTÁTICA COR CINZA MÉDIO (RAL 7046), ACABAMENTO BRILHANTE

CERCAMENTO - VISTA 04

1 : 25

QUADRO DE ESQUADRIAS

CÓD.	LARGURA (cm)	ALTURA (cm)	DESCRIÇÃO	QTD.
			PORTAS	
PT11	220	300	PORTÃO DE GIRO, 2 FOLHAS, ESTRUTURA TUBULAR EM AÇO CARBONO DIÂM.=1 1/2", QUADRO FIXO COM TUBOS DIÂM.=1 '' E VEDAÇÃO EM TELA DE ARAME DE AÇO GALVANIZADO, MALHA 2 '' , FIO Nº 12 BWG E BARRA REDONDA ∅1/2'' . TRINCO DESLIZANTE TIPO FERROLHO PARA CADEADO. APLICAÇÃO DE PINTURA COR CINZA MÉDIO (RAL 7046), ACABAMENTO BRILHANTE.	2

QUADRO ESPECIFICAÇÕES DE ACABAMENTOS

CÓDIGO	DESCRIÇÃO
△	PAREDES
B1	ALVENARIA EM BLOCO DE CONCRETO REVESTIDA COM CHAPISCO, EMBOÇO E REBOCO E SELADOR ACRÍLICO, APLICAÇÃO DE DUAS DEMÃOS DE TINTA LÁTEX ACRÍLICA, ACABAMENTO ACETINADO, COR TERRACOTA, REF.: COR TERRACOTA (CÓD. R118) - SUVINIL OU SIMILAR
B2	ALVENARIA EM BLOCO DE CONCRETO REVESTIDA COM CHAPISCO, EMBOÇO E REBOCO E SELADOR ACRÍLICO, APLICAÇÃO DE DUAS DEMÃOS DE TINTA LÁTEX ACRÍLICA, ACABAMENTO ACETINADO, COR CINZA CLARO (RAL 7035) , REF.: SUVINIL OU SIMILAR
◇	SOLEIRAS, RODAPÉS E PEITORIS
E4	PEITORIL EM CONCRETO PRÉ-MOLDADO, ACABAMENTO LISO, COM PINGADEIRA, ESPESSURA 3cm, ASSENTADO COM ARGAMASSA COLANTE
E6	RODAPÉ EM CONCRETO PRÉ-MOLDADO, ACABAMENTO LISO, ESPESSURA 3cm, H=10cm, ASSENTADO COM ARGAMASSA COLANTE
○	CERCAMENTOS
I2	ALAMBRADO EM ESTRUTURA TUBULAR EM AÇO CARBONO DIÂM.=2", QUADRO FIXO COM TUBOS DIÂM.=1 '' E VEDAÇÃO EM TELA DE ARAME DE AÇO GALVANIZADO, MALHA QUADRADA 50mm (2 ''), FIO Nº 12 BWG E BARRA REDONDA ∅1/2''. APLICAÇÃO DE PINTURA ELETROSTÁTICA COR CINZA MÉDIO (RAL 7046), ACABAMENTO BRILHANTE

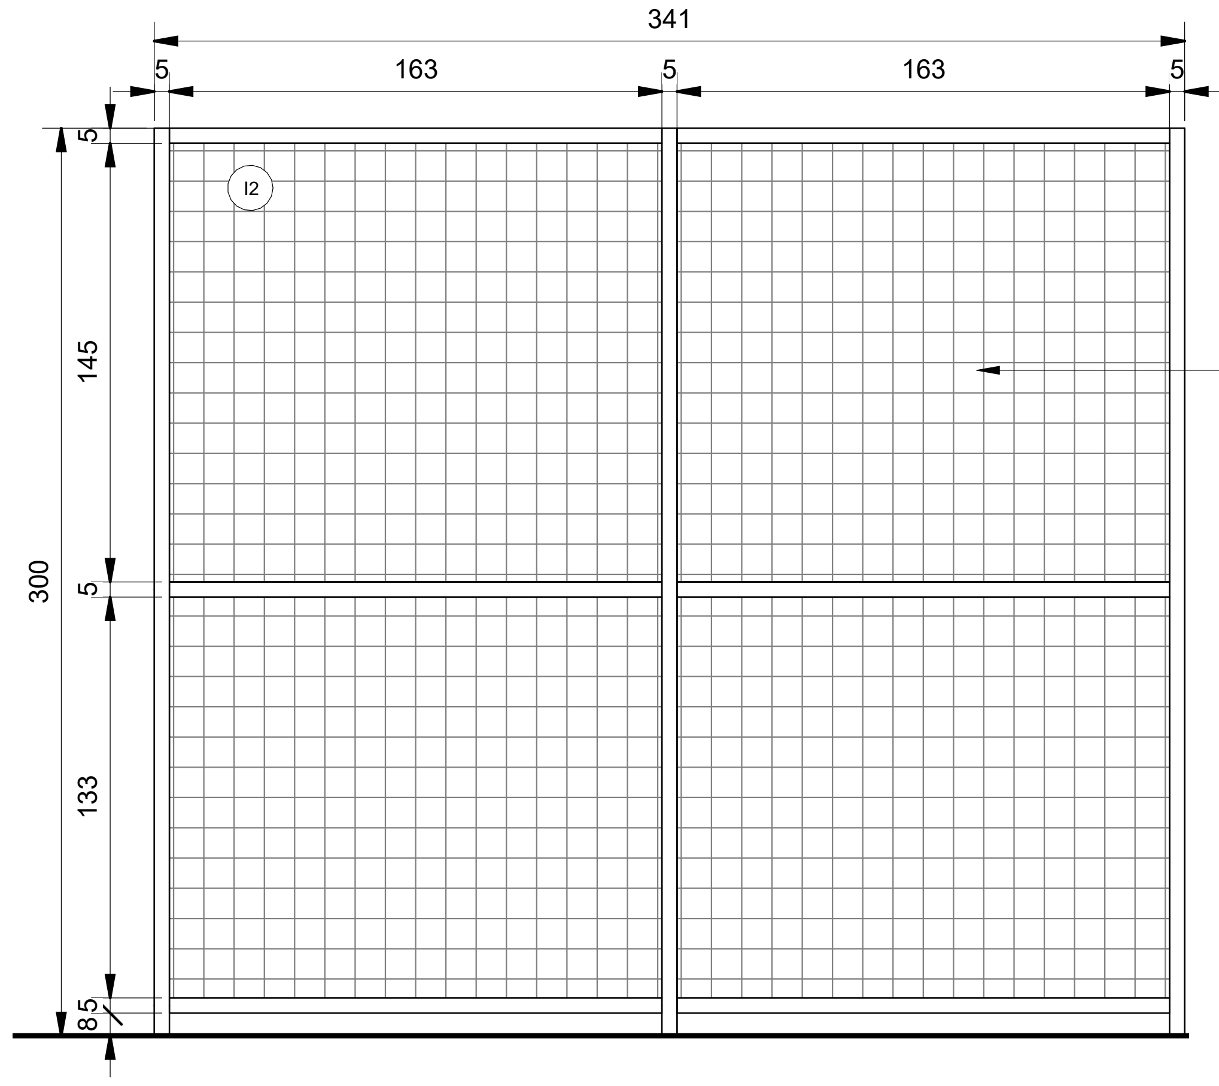

ALAMBRADO EM ESTRUTURA TUBULAR EM AÇO CARBONO DIÂM.=2", QUADRO FIXO COM TUBOS DIÂM.=1'' E VEDAÇÃO EM TELA DE ARAME DE AÇO GALVANIZADO, MALHA QUADRADA 50mm (2''), FIO Nº 12 BWG E BARRA REDONDA ∅1/2''. APLICAÇÃO DE PINTURA ELETROSTÁTICA COR CINZA MÉDIO (RAL 7046), ACABAMENTO BRILHANTE

CERCAMENTO - VISTA 05

1 : 25

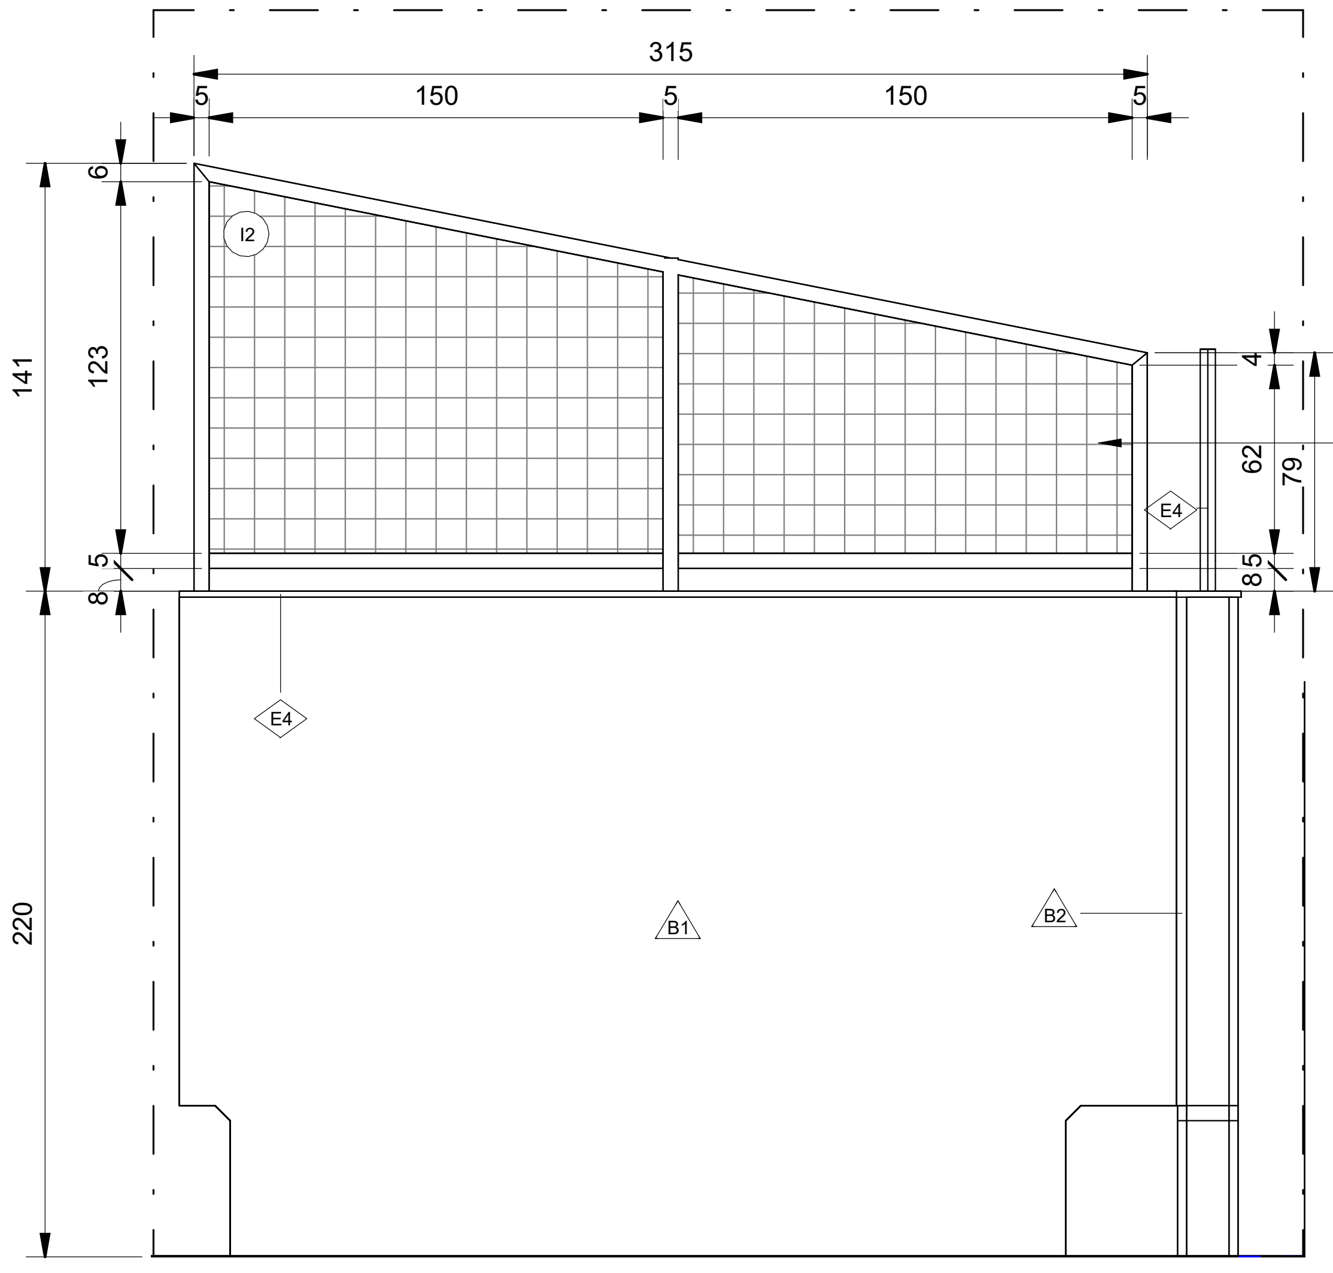

ALAMBRADO EM ESTRUTURA TUBULAR EM AÇO CARBONO DIÂM.=2", QUADRO FIXO COM TUBOS DIÂM.=1'' E VEDAÇÃO EM TELA DE ARAME DE AÇO GALVANIZADO, MALHA QUADRADA 50mm (2''), FIO Nº 12 BWG E BARRA REDONDA ∅1/2''. APLICAÇÃO DE PINTURA ELETROSTÁTICA COR CINZA MÉDIO (RAL 7046), ACABAMENTO BRILHANTE

CERCAMENTO - VISTA 06

1 : 25

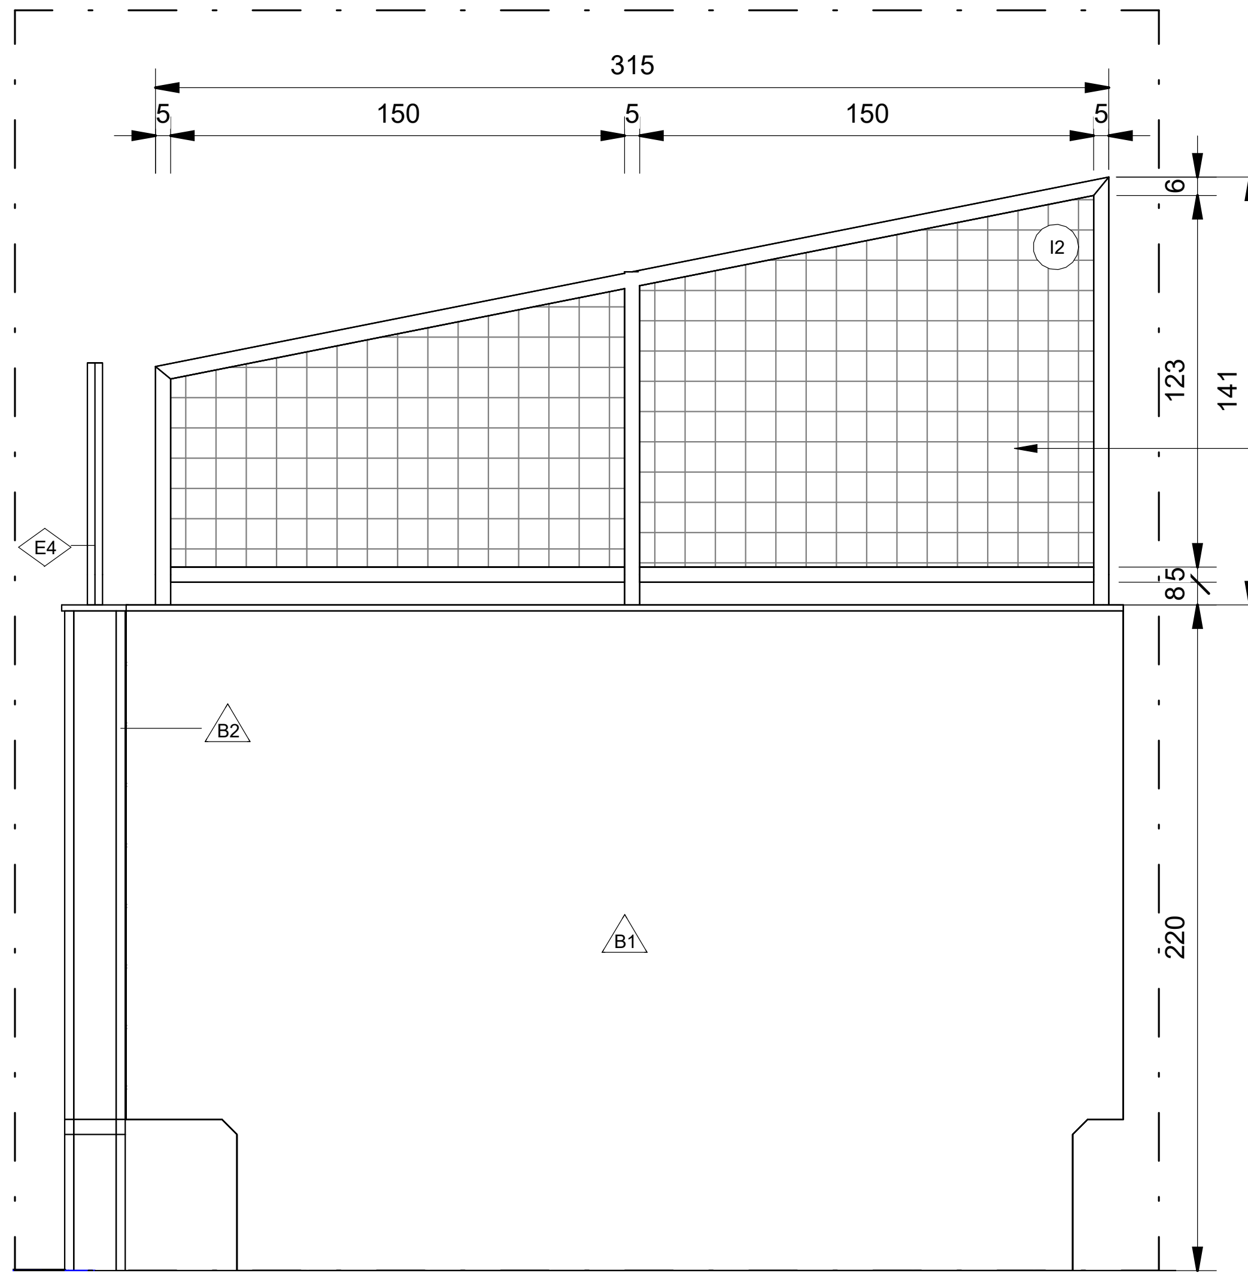

ALAMBRADO EM ESTRUTURA TUBULAR EM AÇO CARBONO DIÂM.=2", QUADRO FIXO COM TUBOS DIÂM.=1'' E VEDAÇÃO EM TELA DE ARAME DE AÇO GALVANIZADO, MALHA QUADRADA 50mm (2''), FIO Nº 12 BWG E BARRA REDONDA ∅1/2''. APLICAÇÃO DE PINTURA ELETROSTÁTICA COR CINZA MÉDIO (RAL 7046), ACABAMENTO BRILHANTE

CERCAMENTO - VISTA 07

1 : 25

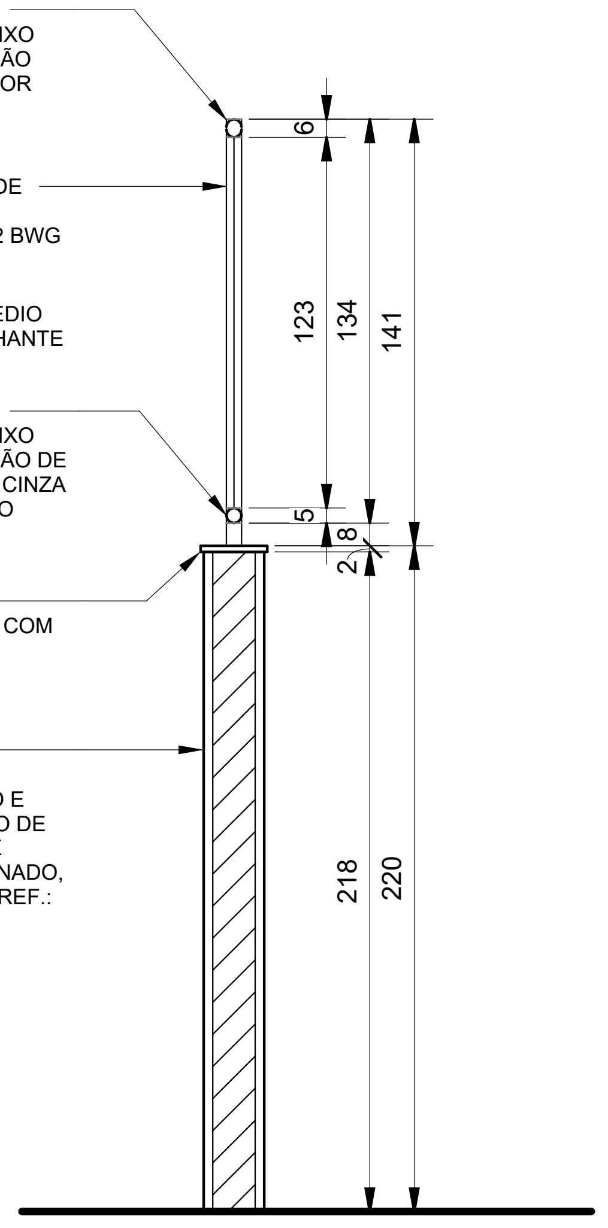

ESTRUTURA TUBULAR EM AÇO CARBONO DIÂM.=2", QUADRO FIXO COM TUBOS DIÂM.=1''. APLICAÇÃO DE PINTURA ELETROSTÁTICA COR CINZA MÉDIO (RAL 7046), ACABAMENTO BRILHANTE

VEDAÇÃO EM TELA DE ARAME DE AÇO GALVANIZADO, MALHA QUADRADA 50mm (2''), FIO Nº 12 BWG E BARRA REDONDA ∅1/2''. APLICAÇÃO DE PINTURA ELETROSTÁTICA COR CINZA MÉDIO (RAL 7046), ACABAMENTO BRILHANTE

ESTRUTURA TUBULAR EM AÇO CARBONO DIÂM.=2", QUADRO FIXO COM TUBOS DIÂM.=1''. APLICAÇÃO DE PINTURA ELETROSTÁTICA COR CINZA MÉDIO (RAL 7046), ACABAMENTO BRILHANTE

PEITORIL EM CONCRETO PRÉ-MOLDADO, ACABAMENTO LISO, COM PINGADEIRA, ESPESSURA 3cm, ASSENTADO COM ARGAMASSA COLANTE

ALVENARIA EM BLOCO DE CONCRETO REVESTIDA COM CHAPISCO, EMBOÇO E REBOCO E SELADOR ACRÍLICO, APLICAÇÃO DE DUAS DEMÃOS DE TINTA LÁTEX ACRÍLICA, ACABAMENTO ACETINADO, COR CINZA CLARO (RAL 7035) , REF.: SUVINIL OU SIMILAR

CERCAMENTO - CORTE TÍPICO

1 : 25

CODIFICAÇÃO AWP – ADVANCED WORK PACKAGING

CWA	CÓDIGOS:	CWA 001 - PLATÔ DOS PRÉDIOS OPERACIONAIS
CWP	CÓDIGOS:	CWP 007 - OFICINA AVANÇADA G1342ED08-CWA 001-G-MT-0001.007-CWP 007
EWP	CÓDIGOS:	G1342ED08-CWA 001-G-MT-0001.007-EWP 007

NOTAS

1- DIMENSÕES EM CENTÍMETROS, ELEVAÇÕES E COORDENADAS EM METRO, SALVO INDICAÇÃO EM CONTRÁRIO;
2 - AS ELEVAÇÕES APRESENTADAS EM PROJETO CORRESPONDEM AO NÍVEL DO PISO ACABADO;
3 - PARA ESPECIFICAÇÕES DETALHADAS DOS MATERIAIS E ACABAMENTOS, VER CADERNO DE ESPECIFICAÇÕES DA SAMARCO (DOCUMENTO Nº T000000-G-6NT004);
4 - PARA AS PAREDES EXTERNAS E INTERNAS DA OFICINA SERÃO UTILIZADOS BLOCOS DE CONCRETO COM ESPESSURA DE 14cm.
5 - A ELEVAÇÃO 0,00 NO PROJETO CORRESPONDE À COTA +823,00 DO PROJETO DE INFRAESTRUTURA (DOCUMENTO SAMARCO Nº G134448-O-1000105).
6 - O ESCOPO DA DISCIPLINA DE ARQUITETURA NA OFICINA AVANÇADA SE LIMITA AS DEFINIÇÕES DOS CERCAMENTOS, ALAMBRADOS, ESQUADRIAS, ALVENARIAS E ACABAMENTOS. A DISPOSIÇÃO DOS AMBIENTES INTERNOS, O LAYOUT, E OS ACESSOS FORAM DEFINIDOS PELA MECÂNICA.
7 - AS ALVENARIAS DE DIVISÃO ENTRE O DEPÓSITO DE TAMBORES E O COMPRESSOR, E ENTRE O DEPÓSITO E A OFICINA DEVERÃO POSSUIR PROPRIEDADES CORTA-FOGO, CONFORME IT-06 DO CBMMG. DESTA FORMA, DEVERÃO SER EXECUTADAS COM BLOCO DE CONCRETO DE 14cm DE ESPESSURA, COM UMA CAMADA DE CHAPISCO E EMBOÇO DE NO MÍNIMO 1,5cm.
8 - PARA LAYOUT DA OFICINA AVANÇADA, VER DOCUMENTO MECÂNICA NºG134211-M-100039.
9 - A ESCADA DE MARINHEIRO PARA ACESSO À COBERTURA DEVERÁ SEGUIR AS PREMISSAS DOCUMENTO DE SEGURANÇA DA SAMARCO Nº T000002-S-2PS004;

DESENHOS DE REFERÊNCIA

1 - IMPLANTAÇÃO DA ARQUITETURA - DOC. Nº G134140-C-800038
2 - DESENHOS COMPLEMENTARES G134240-C-800030 / G134240-C-800031 / G134240-C-800032 / G134240-C-8000XX
3 - DETALHAMENTO DE ESQUADRIAS - DOC. Nº G130000-C-800001 / G130000-C-800002 / G130000-C-800003 / G130000-C-800004

ESPESSURA DE LINHAS DA SAMARCO
1 – RED – 0,10mm
2 – YELLOW – 0,5mm
3 – GREEN – 0,20mm
4 – CYAN – 0,30mm
5 – BLUE – 0,15mm
6 – MAGENTA – 0,60mm
7 – WHITE – 0,40mm
8 – CINZA – 0,80mm

ESPESSURA DE LINHAS EXTRAS ADOTADAS NESTE DESENHO SAMARCO

17	18	19
20	21	22
23	24	25